


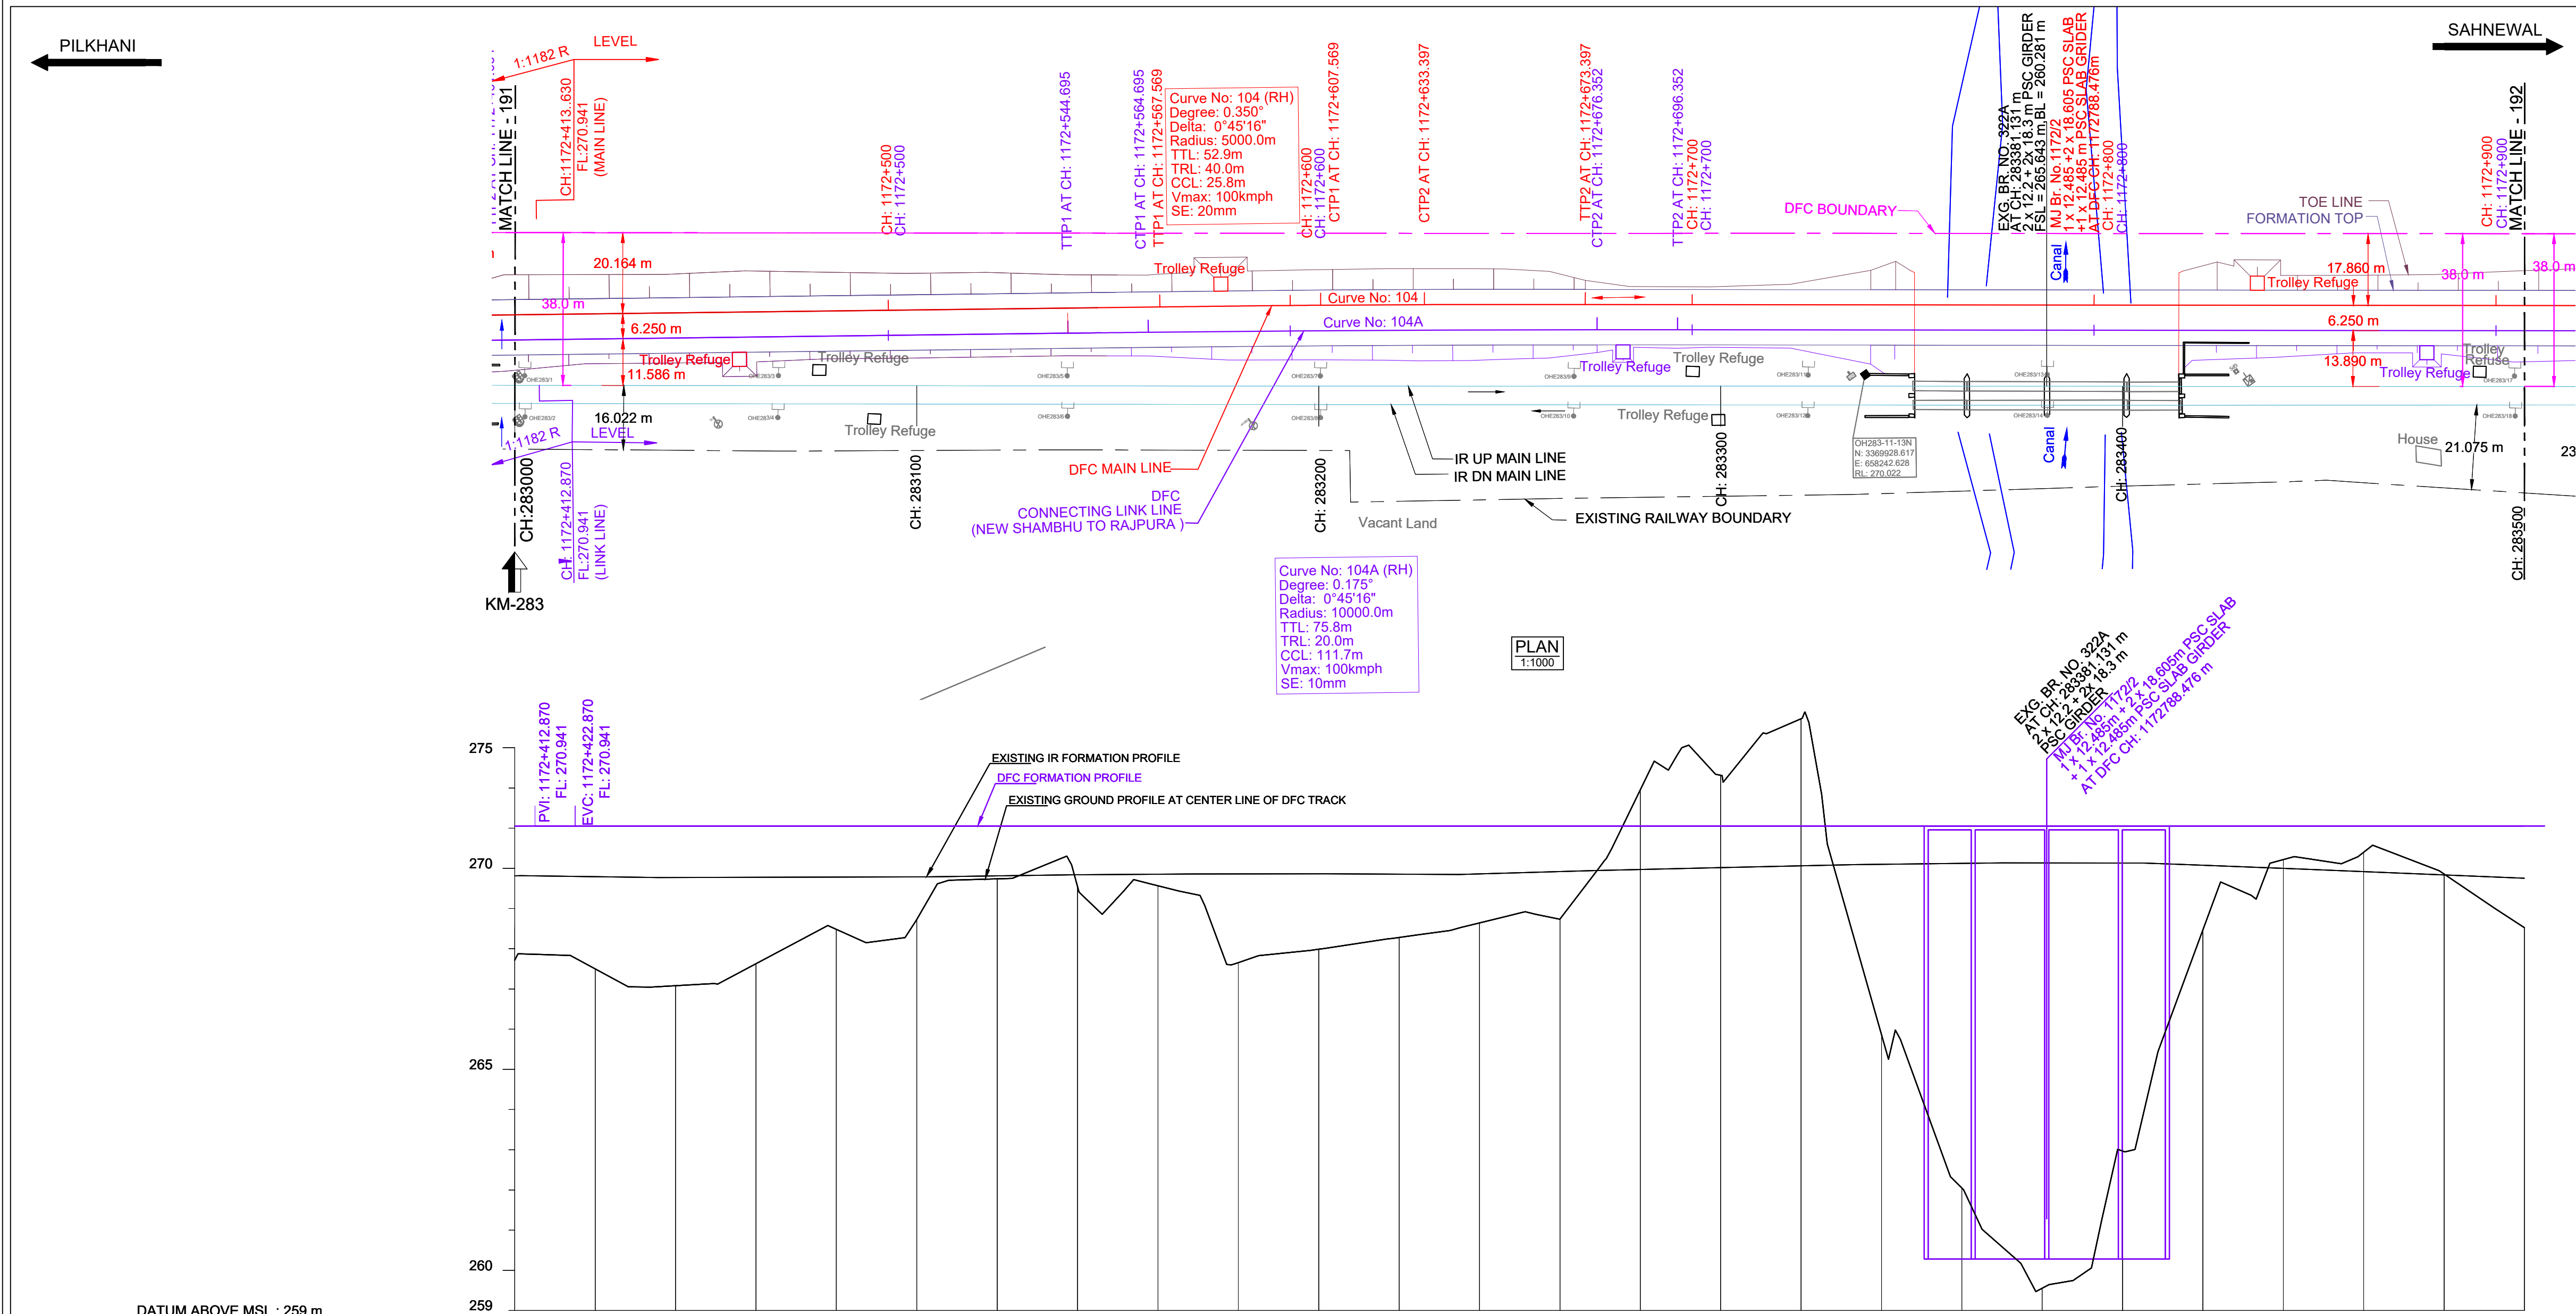

HORIZONTAL ALIGNMENT		L = 143.631m TL= 20m R =10000m TL= 20m L = 234.666m																											
VERTICAL ALIGNMENT		L=20.0 m R=23650 m L=620.095 m LEVEL																											
TRACK DISTANCE FROM EXISTING NEAREST IR UP MAIN LINE TO DFC LINKED LINE		11.289	-11.289	-11.566	-11.841	-12.111	-12.370	-12.620	-12.880	-13.140	-13.384	-13.602	-13.762	-13.896	-13.986	-14.021	-14.014	-13.985	-13.963	-13.950	-13.956	-13.951	-13.934	-13.926	-13.902	-13.891	-13.884	-13.877	
HEIGHT OF BANKING(+) / DEPTH OF CUTTING(-) (PFL-GL)		+3.335	+3.335	+3.557	+3.975	+3.429	+2.573	-2.329	+1.317	+1.505	+1.486	+3.400	-3.065	+2.774	-2.412	+2.319	-0.890	-1.260	-2.662	+5.177	-265.764	-261.941	-259.440	-262.856	-268.342	-0.839	-0.657	+1.194	-2.526
EXG GROUND LEVEL AT CENTER LINE OF DFC TRACK (GL)		267.601	267.601	267.384	266.966	267.512	268.368	268.612	269.624	269.636	269.455	267.541	268.876	268.167	268.529	268.622	271.831	272.201	273.803	265.764	265.451	261.941	259.440	262.856	268.342	270.102	270.284	269.747	268.415
EXG GROUND LEVEL AT TOE LOCATION OF DFC TRACK		267.376	267.376	267.070	266.417	266.932	267.174	268.529	269.043	268.753	269.175	268.322	268.008	267.992	268.230	268.984	271.754	272.685	272.810	267.451	262.136	259.098	262.351	267.050	269.893	270.115	270.318	268.419	268.415
DIFFERENCE BETWEEN DFC FORMATION LEVEL AND EXG.FORMATION LEVEL.(PFL-EFL)		1.242	1.242	1.264	1.283	1.277	1.272	1.267	1.241	1.213	1.199	1.192	1.192	1.200	1.192	1.133	1.082	1.036	0.992	0.955	0.931	0.920	0.924	0.976	1.056	1.137	1.218	1.299	
DFC FORMATION LEVEL (PFL)		270.936	270.936	270.941	270.941	270.941	270.941	270.941	270.941	270.941	270.941	270.941	270.941	270.941	270.941	270.941	270.941	270.941	270.941	270.941	270.941	270.941	270.941	270.941	270.941	270.941	270.941	270.941	270.941
EXG. FORMATION LEVEL OF EXG IR UP MAIN LINE (EFL)		269.695	269.695	269.677	269.658	269.664	269.669	269.674	269.700	269.728	269.742	269.749	269.749	269.741	269.749	269.808	269.859	269.905	269.949	269.986	270.010	270.021	270.017	269.965	270.021	270.061	269.804	269.723	269.642
DIFFERENCE BETWEEN DFC RAIL LEVEL AND EXG. RAIL LEVEL (PRL - ERL)		1.267	1.267	1.289	1.308	1.302	1.297	1.292	1.266	1.238	1.224	1.217	1.217	1.225	1.217	1.158	1.107	1.061	1.017	0.980	0.956	0.945	0.949	1.001	1.081	1.162	1.243	1.324	
DFC RAIL LEVEL (PRL)		271.649	271.649	271.654	271.654	271.654	271.654	271.654	271.654	271.654	271.654	271.654	271.654	271.654	271.654	271.654	271.654	271.654	271.654	271.654	271.654	271.654	271.654	271.654	271.654	271.654	271.654	271.654	271.654
EXG.RAIL LEVEL OF NEAREST IR UP MAIN LINE(ERL)		270.383	270.383	270.365	270.346	270.352	270.357	270.362	270.388	270.416	270.430	270.437	270.437	270.429	270.437	270.496	270.547	270.593	270.637	270.674	270.698	270.709	270.705	270.692	270.653	270.573	270.411	270.330	270.330
EQUIVALENT CHAINAGE ON DFC TRACK		1172407.3	1172407.3	1172427.3	1172447.3	1172467.3	1172487.3	1172507.3	1172527.3	1172547.3	1172567.3	1172587.3	1172607.3	1172627.3	1172647.3	1172667.3	1172687.3	1172707.3	1172727.3	1172747.3	1172767.3	1172787.3	1172807.3	1172827.3	1172847.3	1172867.3	1172887.3	1172907.3	1172927.3
EXISTING IR CHAINAGE		283000.0	283000.0	283020.0	283040.0	283060.0	283080.0	283100.0	283120.0	283140.0	283160.0	283180.0	283200.0	283220.0	283240.0	283260.0	283280.0	283300.0	283320.0	283340.0	283360.0	283380.0	283400.0	283420.0	283440.0	283460.0	283480.0	283500.0	283520.0

L - SECTION