


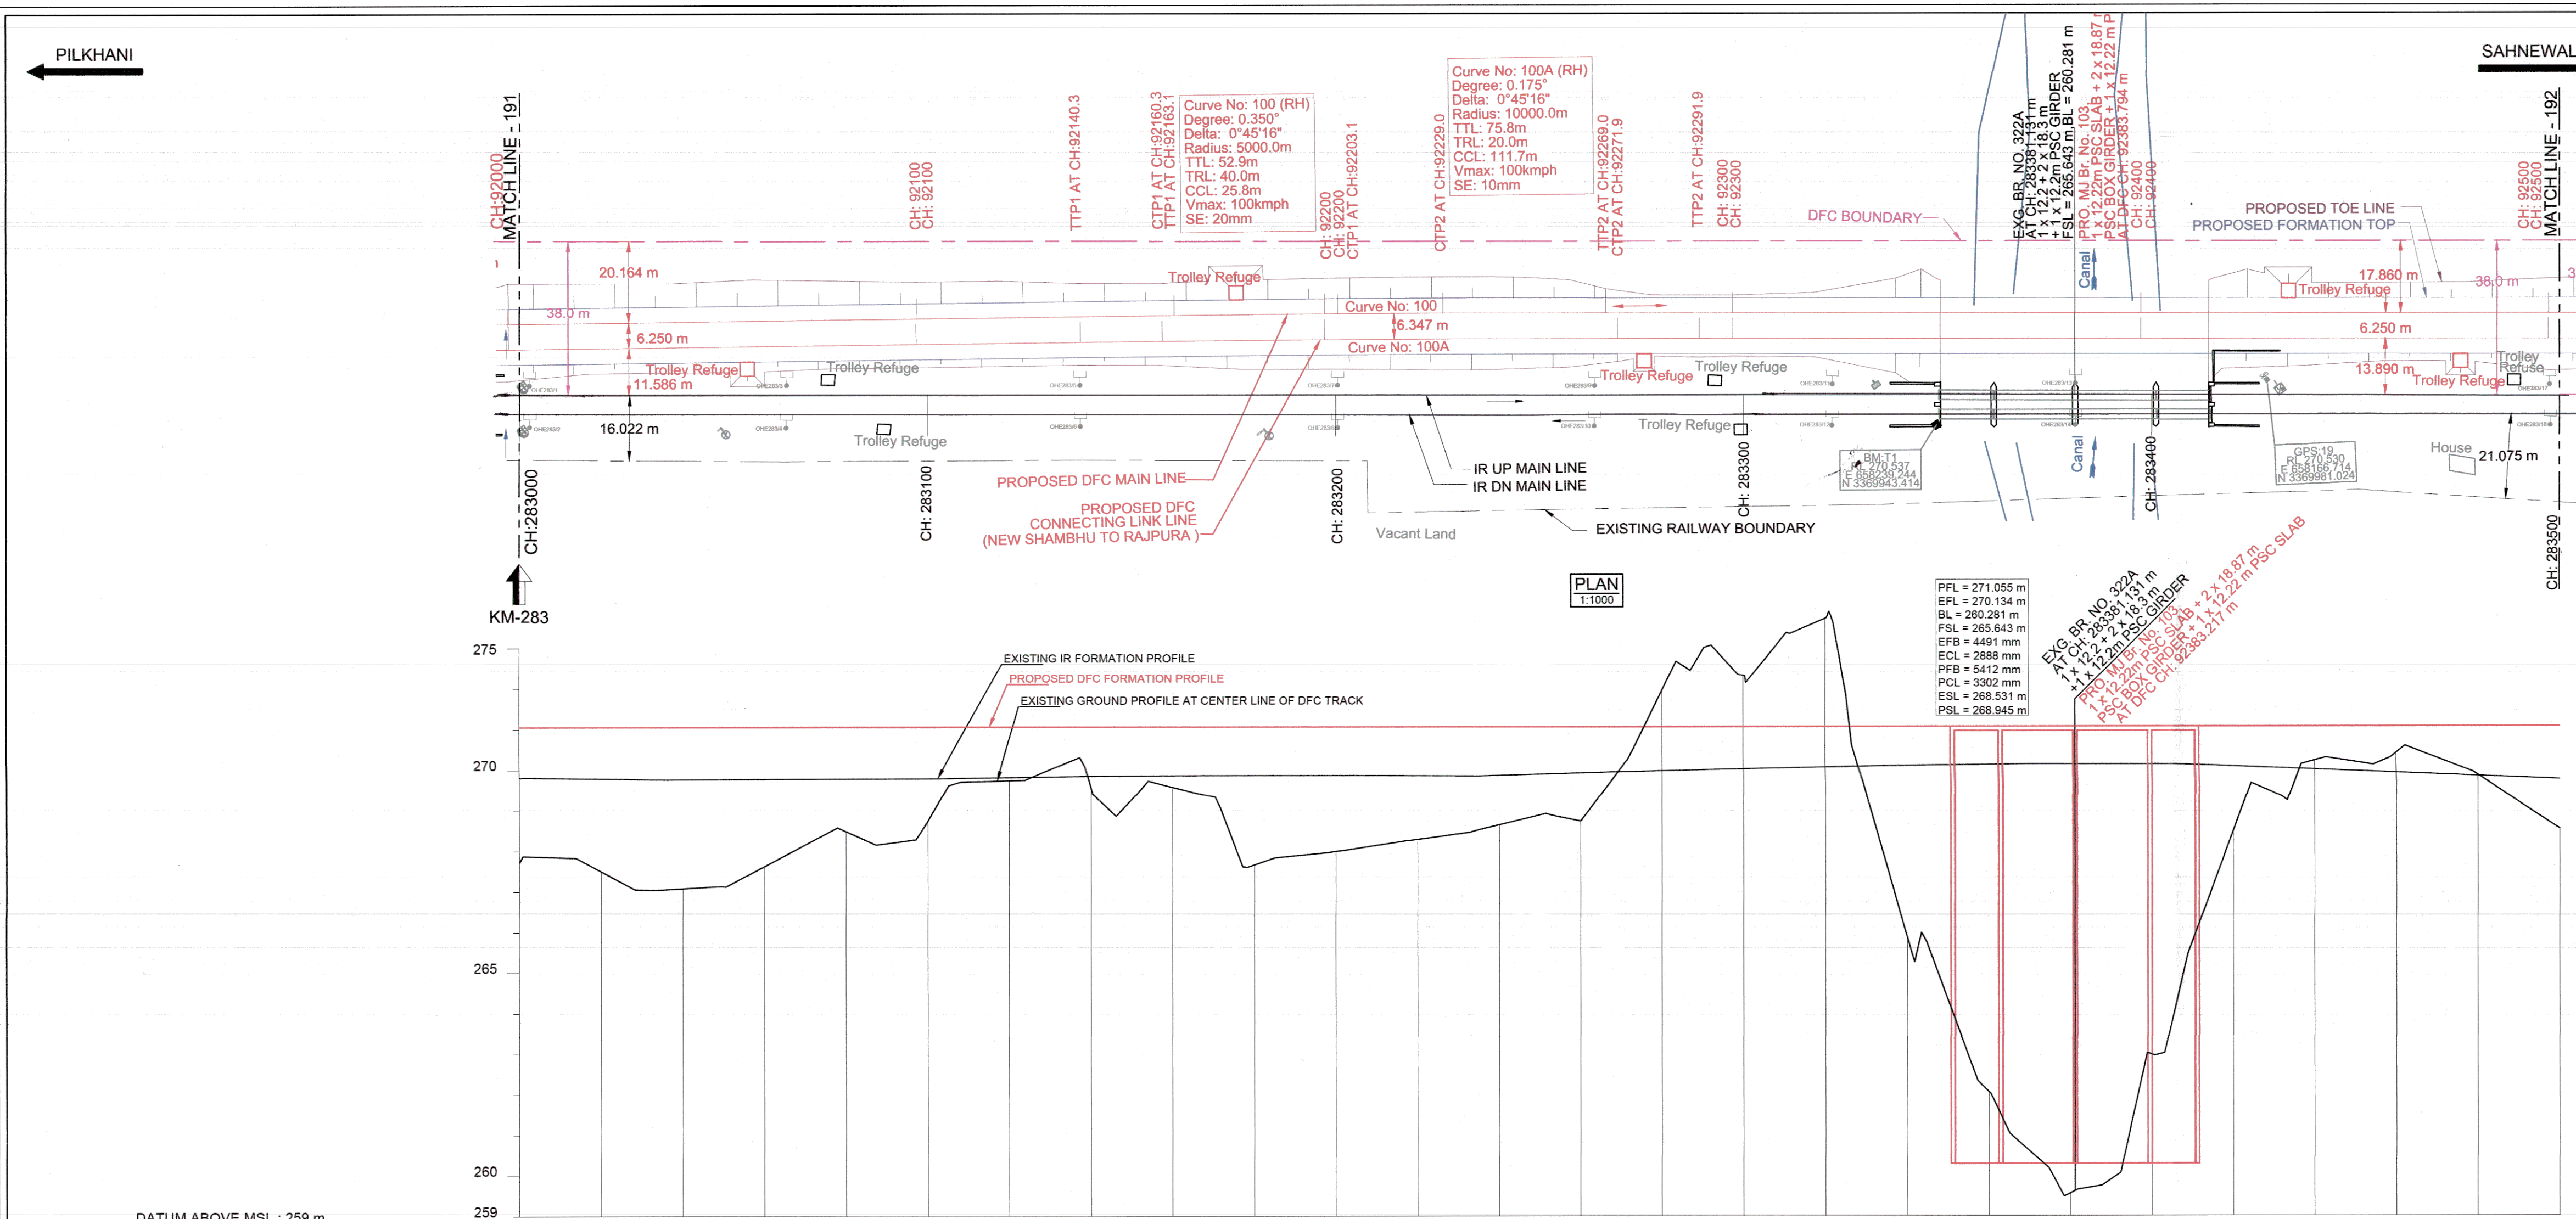


DATUM ABOVE MSL : 259 m

HORIZONTAL ALIGNMENT		L = 143.632m		TL= 20m		R =10000m		TL= 20m		L = 234.666m	
VERTICAL ALIGNMENT		L=758.1 m LEVEL									
TRACK DISTANCE FROM EXISTING NEAREST IR UP MAIN LINE TO PROPOSED DFC LINKED LINE		11.289									
HEIGHT OF BANKING(+) / DEPTH OF CUTTING(-) (PFL-GL)		+3.336									
EXG GROUND LEVEL AT CENTER LINE OF PRO. DFC TRACK (GL)		267.719									
EXG GROUND LEVEL AT TOE LOCATION OF PRO. DFC TRACK		267.496									
DIFFERENCE BETWEEN PRO FORMATION LEVEL AND EXG.FORMATION LEVEL.(PFL-EFL)		1.242									
PRO. DFC FORMATION LEVEL (PFL)		271.055									
EXG. FORMATION LEVEL OF EXG IR UP MAIN LINE (EFL)		269.813									
DIFFERENCE BETWEEN PRO. DFC RAIL LEVEL AND EXG. RAIL LEVEL (PRL - ERL)		1.296									
PRO. DFC RAIL LEVEL (PRL)		271.797									
EXG.RAIL LEVEL OF NEAREST IR UP MAIN LINE(ERL)		270.501									
EQUIVALENT CHAINAGE ON PROPOSED DFC TRACK		92002.7									
EXISTING IR CHAINAGE		283000.0									

L - SECTION (CONNECTING LINK LINE)

REV.	DATE	REVISION DETAILS	PURPOSE OF ISSUE
2	26.03.18	UPDATED AS PER PMC COMMENTS	FOR APPROVAL
1	16.03.18	COMPLIANCE TO PMC COMMENTS, DI 30.12.17	FOR APPROVAL
0	13.12.17	INITIAL SUBMISSION	FOR APPROVAL

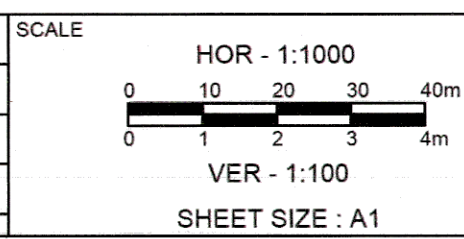

DESIGN CONSULTANT
aarvee associates
architects engineers & consultants pvt.ltd

CONTRACTOR
GIL - TPL JV

ENGINEER
DB Engineering & Consulting GmbH

CONTRACTOR
B.RAMAKRISHNA
DESIGNED

CONTRACTOR
H.B.PANDA
CHECKED

CONTRACTOR
DINESH PANDAY
APPROVED

ENGINEER
BABUL SAHU
REVIEWED

ENGINEER
H.D.VIDYAK
NONG

TITLE PLAN & PROFILE FROM IR KM: 283.000 TO 283.500 FROM DFC KM: 92.003 TO 92.503 (CONNECTING LINK LINE)		DFCC APPR. NO. - ENG APPR. NO. - DRG. NO. - 301-2/AL/1192A SHEET NO. : 192A OF 346 DATE : 26.03.2018	REV. No. 2	STATUS D
--	--	--	---------------	-------------

WITH NEW GTS VALUE

SHEET NO. : 192A OF 346

NOTE:

- PROPOSED WORKS ARE SHOWN IN RED.
- IR PROPOSALS ARE SHOWN IN VIOLET.
- ALL DIMENSIONS ARE SHOWN IN METRES.
- THIS DRAWING IS PREPARED BASED ON LATEST SURVEY DATA HELD ON AUG-2016. GTS BENCH MARK OF 261.850 m CONSIDERED ON TOP OF CANAL BRIDGE ABUTMENT AT DORAHA VILLAGE ALONG THE NH1.
- MINIMUM OF 6m TRACK CENTER MAINTAINED BETWEEN ADJACENT TRACK TO EXISTING IR TRACK IN STATION YARD PORTION.
- DFC CHANGAGE OF 0.000 m IS WITH REFERENCE TO THE IR KM POST OF 192.000
- PUBLIC UTILITIES, HT, LT LINES AND OFC CABLES, WATER LINES etc., INTERFERING DFC LINES SHALL BE RELOCATED.
- PLAN OF LONGITUDINAL AS WELL AS CROSS DRAINAGE WORKS BETWEEN IR & DFC BANKS SHALL BE SUBMITTED SEPARATELY FOR APPROVAL
- ALL CANAL BRIDGES REQUIRED TO BE APPROVED BY CANAL AUTHORITIES.
- NECESSARY EMBANKMENT/SLOPE PROTECTION WORK DESIGN & DRAWING WILL BE SUBMITTED SEPARATELY
- UNDERTAKING OF NO EXTRA CLAIM FOR DESIGN & EXECUTION OF WORK DUE TO CHANGE IN TURNOUT LENGTH AND DRAINAGE DESIGN HAS BEEN GIVEN BY GIL-TPL
- J/EDFC/301/2017-18/DESIGN/0424 DATED 28.07.2017
- DURING CENTER LINE STAKING IF GROUND LEVEL SHOWN, FOUND TO BE MAJOR VARIATION, DESIGNER TO BE INFORMED.
- THE LAND BOUNDARY SHOWN IN THE ALIGNMENT DRAWING IS TENTATIVE ONLY. FOR ACTUAL ACQUISITION REFER LAND PLANS OF THAT CORRESPONDING SECTION.
- FOR DETAILS OF DFC MAIN LINE FROM NEW SHAMBHU TO RAJUPURA REFER SEPARATE DRAWINGS.
- SR. NO. 322A/103 DATA PROVIDED AS PER PRELIMINARY DRAWING NO. 301-1/RB/1562 TO 301-1/RB/1564.
- LOCATIONS PRONE TO FLOODING IN THE SECTION: NO
- WATER LOGGED AREA/ MARSHY LAND WHERE GROUND IMPROVEMENT REQUIRED: NO
- LOCATION OF TROLLEY REFUGE SHOWN ARE INDICATIVE, WILL BE FINALISED SEPARATELY.

REFERENCE DRAWINGS :-

- FOR KEY PLAN REFER DRAWING NO. 301-2/AL/0001.
- FOR LEGEND AND ABBREVIATIONS REFER DRAWING NO. 301-2/AL/1000.

THIS CONSTRUCTION DRAWING OF PLAN & PROFILE IS PREPARED BASED ON PRELIMINARY DRAWING APPROVAL BY DFCCIL COMMUNICATED UNDER LETTER NO. EDFC 3/PMC/CON/11/2017/0715 DATED : 20.11.2017

TRACK STRUCTURE		
RAIL SECTION: 60Kg/m (UIC 60Kg/m) DFC LINE: 60Kg/m (UIC 60Kg/m) IR MAIN LINE: 52Kg/m	Difference between FL and RL	
	IR Line	DFC
RUBBER PAD	172mm	172mm
SLEEPER DEPTH	210mm	210mm
BALLAST CUSHION	300mm	350mm
Total Depth (FL TO RL)	688mm	742mm

PROJECT OFFICE / DFCCIL		
SURINDER PAL CPM		
PARDEEP PURI DY. CPM / ENGS. / LDH	P.KATHALIA ACPM / ELECT. / UMB	
CHANKY GARG PM / ELECT. / UMB	ABHINAV SINGH PM / S&T	
SURENDRA SINGH DPM / ENGS. / UMB	S.P. SHARMA DPM / ELECT. / UMB	DEBASISH NAYAK APM / S&T-II / UMB

OWNER DEDICATED FREIGHT CORRIDOR CORPORATION OF INDIA LTD. (A GOVERNMENT OF INDIA ENTERPRISE) PROJECT OFFICE (AMBALA UNIT), OLD RAILWAY COLONY (NEAR ANAND MARKET), AMBALA CANTT-133001 CORPORATE IDENTITY NO. : U60232DL2006001155068	PROJECT EASTERN DEDICATED FREIGHT CORRIDOR SAHNEWAL TO PILKHANI CONTRACT PACKAGE - 301	
--	---	--