


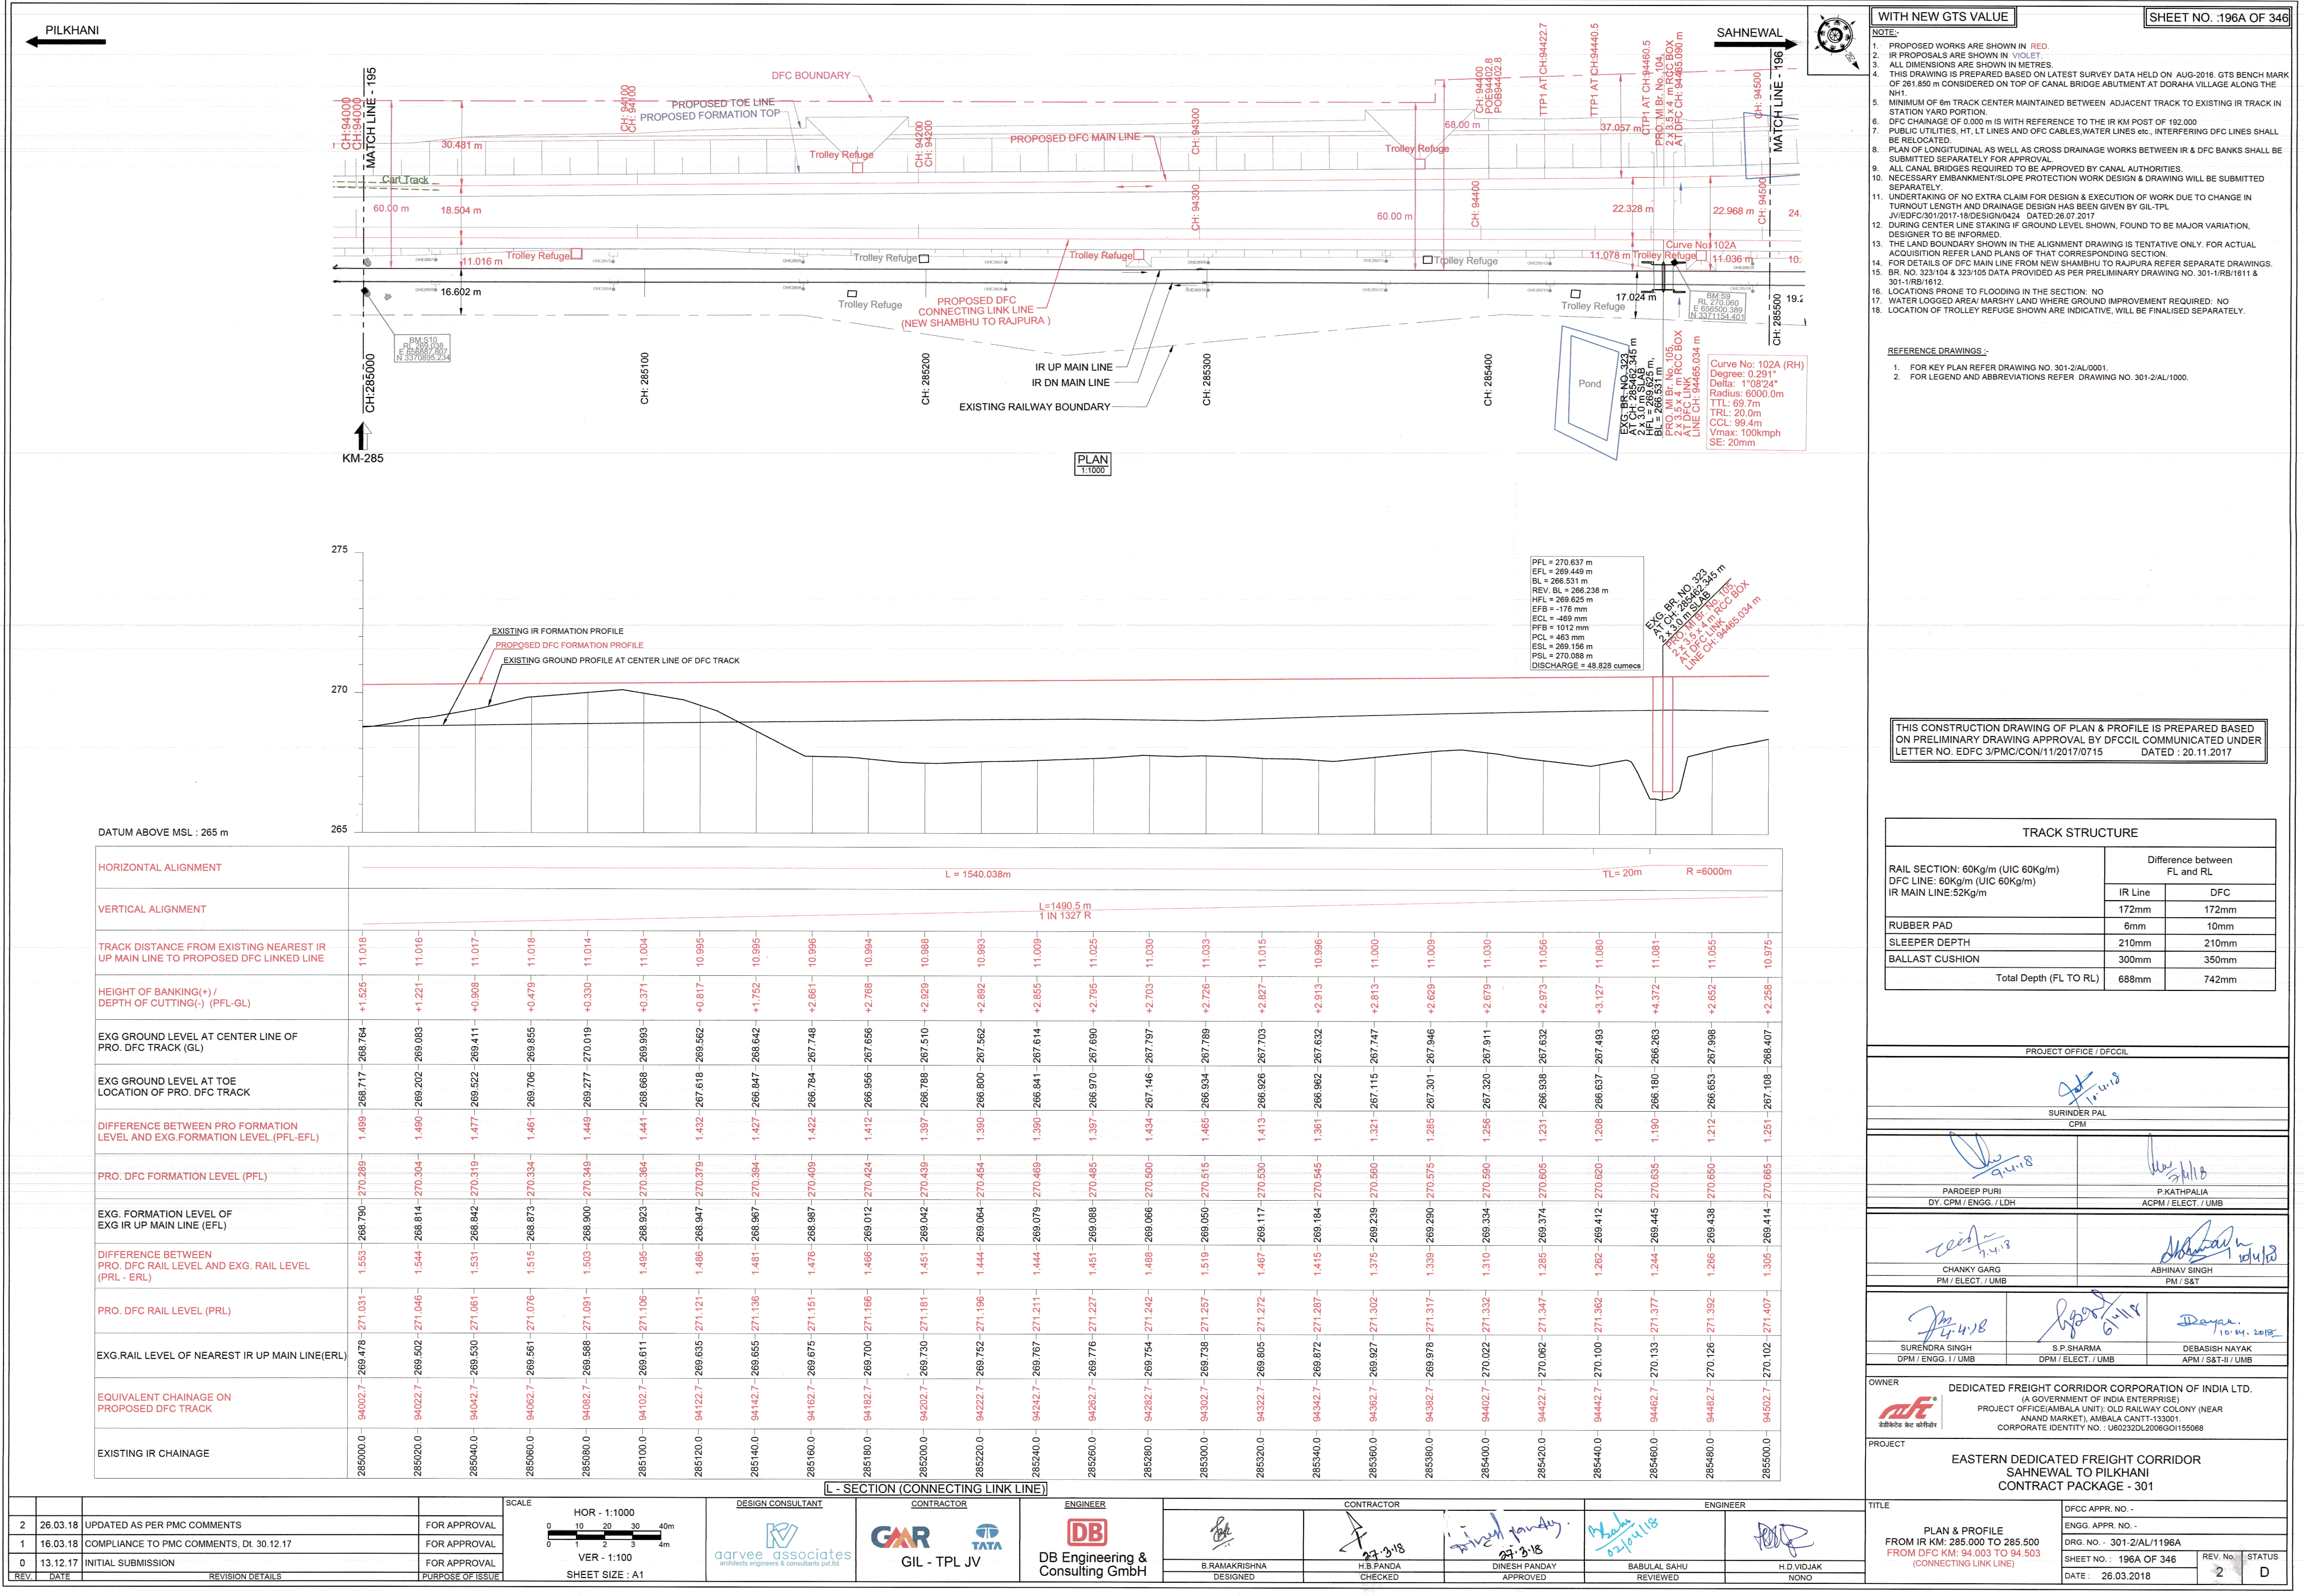

WITH NEW GTS VALUE

SHEET NO. :196A OF 346

NOTE:-

- PROPOSED WORKS ARE SHOWN IN RED.
- IR PROPOSALS ARE SHOWN IN VIOLET.
- ALL DIMENSIONS ARE SHOWN IN METRES.
- THIS DRAWING IS PREPARED BASED ON LATEST SURVEY DATA HELD ON AUG-2016. GTS BENCH MARK OF 261.850 m CONSIDERED ON TOP OF CANAL BRIDGE ABUTMENT AT DORAHA VILLAGE ALONG THE NH1.
- MINIMUM OF 6m TRACK CENTER MAINTAINED BETWEEN ADJACENT TRACK TO EXISTING IR TRACK IN STATION YARD PORTION.
- DFC CHAINAGE OF 0.000 m IS WITH REFERENCE TO THE IR KM POST OF 192.000.
- PUBLIC UTILITIES, HT, LT LINES AND OFC CABLES, WATER LINES ETC., INTERFERING DFC LINES SHALL BE RELOCATED.
- PLAN OF LONGITUDINAL AS WELL AS CROSS DRAINAGE WORKS BETWEEN IR & DFC BANKS SHALL BE SUBMITTED SEPARATELY FOR APPROVAL.
- ALL CANAL BRIDGES REQUIRED TO BE APPROVED BY CANAL AUTHORITIES.
- NECESSARY EMBANKMENT/SLOPE PROTECTION WORK DESIGN & DRAWING WILL BE SUBMITTED SEPARATELY.
- UNDERTAKING OF NO EXTRA CLAIM FOR DESIGN & EXECUTION OF WORK DUE TO CHANGE IN TURNOUT LENGTH AND DRAINAGE DESIGN HAS BEEN GIVEN BY GIL-TPL JV/EDFC/301/2017-18/DESIGN/0424 DATED 26.07.2017.
- DURING CENTER LINE STAKING IF GROUND LEVEL SHOWN, FOUND TO BE MAJOR VARIATION, DESIGNER TO BE INFORMED.
- THE LAND BOUNDARY SHOWN IN THE ALIGNMENT DRAWING IS TENTATIVE ONLY. FOR ACTUAL ACQUISITION REFER LAND PLANS OF THAT CORRESPONDING SECTION.
- FOR DETAILS OF DFC MAIN LINE FROM NEW SHAMBHU TO RAJUPURA REFER SEPARATE DRAWINGS.
- BR. NO. 323/104 & 323/105 DATA PROVIDED AS PER PRELIMINARY DRAWING NO. 301-1/RB/1611 & 301-1/RB/1612.
- LOCATIONS PRONE TO FLOODING IN THE SECTION: NO.
- WATER LOGGED AREA/MARSHY LAND WHERE GROUND IMPROVEMENT REQUIRED: NO.
- LOCATION OF TROLLEY REFUGE SHOWN ARE INDICATIVE, WILL BE FINALISED SEPARATELY.

REFERENCE DRAWINGS:-

- FOR KEY PLAN REFER DRAWING NO. 301-2/AL/0001.
- FOR LEGEND AND ABBREVIATIONS REFER DRAWING NO. 301-2/AL/1000.

THIS CONSTRUCTION DRAWING OF PLAN & PROFILE IS PREPARED BASED ON PRELIMINARY DRAWING APPROVAL BY DFCIL COMMUNICATED UNDER LETTER NO. EDFC 3/PMC/CON/11/2017/0715 DATED : 20.11.2017

TRACK STRUCTURE		
RAIL SECTION: 60Kg/m (UIC 60Kg/m) DFC LINE: 60Kg/m (UIC 60Kg/m) IR MAIN LINE: 52Kg/m	Difference between FL and RL	
	IR Line	DFC
RUBBER PAD	6mm	10mm
SLEEPER DEPTH	210mm	210mm
BALLAST CUSHION	300mm	350mm
Total Depth (FL TO RL)	688mm	742mm

PROJECT OFFICE / DFCIL

SURINDER PAL
CPM

PARDEEP PURI
DY. CPM / ENGG. / LDH

P. KATHPALIA
ACPM / ELECT. / UMB

CHANKY GARG
PM / ELECT. / UMB

ABHINAV SINGH
PM / S&T

SURENDRA SINGH
DPM / ENGG. / UMB

S.P. SHARMA
DPM / ELECT. / UMB

DEBASISH NAYAK
APM / S&T-II / UMB

OWNER: DEDICATED FREIGHT CORRIDOR CORPORATION OF INDIA LTD. (A GOVERNMENT OF INDIA ENTERPRISE)
PROJECT OFFICE: AMBALA UNIT, OLD RAILWAY COLONY (NEAR ANAND MARKET), AMBALA CANTT-133001.
CORPORATE IDENTITY NO.: U60232DL200601155068

PROJECT: EASTERN DEDICATED FREIGHT CORRIDOR SAHNEWAL TO PILKHANI CONTRACT PACKAGE - 301

REV	DATE	REVISION DETAILS	PURPOSE OF ISSUE
2	26.03.18	UPDATED AS PER PMC COMMENTS	FOR APPROVAL
1	16.03.18	COMPLIANCE TO PMC COMMENTS, Dt. 30.12.17	FOR APPROVAL
0	13.12.17	INITIAL SUBMISSION	FOR APPROVAL

SCALE: HOR - 1:1000
VER - 1:100
SHEET SIZE: A1

DESIGN CONSULTANT: aarvee associates architects engineers & consultants pvt.ltd.

CONTRACTOR: GIL - TPL JV

ENGINEER: DB Engineering & Consulting GmbH

CONTRACTOR: H.B. PANDA
CHECKED: DINESH PANDAY
APPROVED: BABULAL SAHU
REVIEWED: H.D. VIDJAK
NONO

TITLE: PLAN & PROFILE FROM IR KM: 285.000 TO 285.500 FROM DFC KM: 94.003 TO 94.503 (CONNECTING LINK LINE)

DFCC APPR. NO.: ENGG. APPR. NO.: DRG. NO.: 301-2/AL/1196A
SHEET NO.: 196A OF 346
DATE: 26.03.2018

REV No.: 2
STATUS: D