


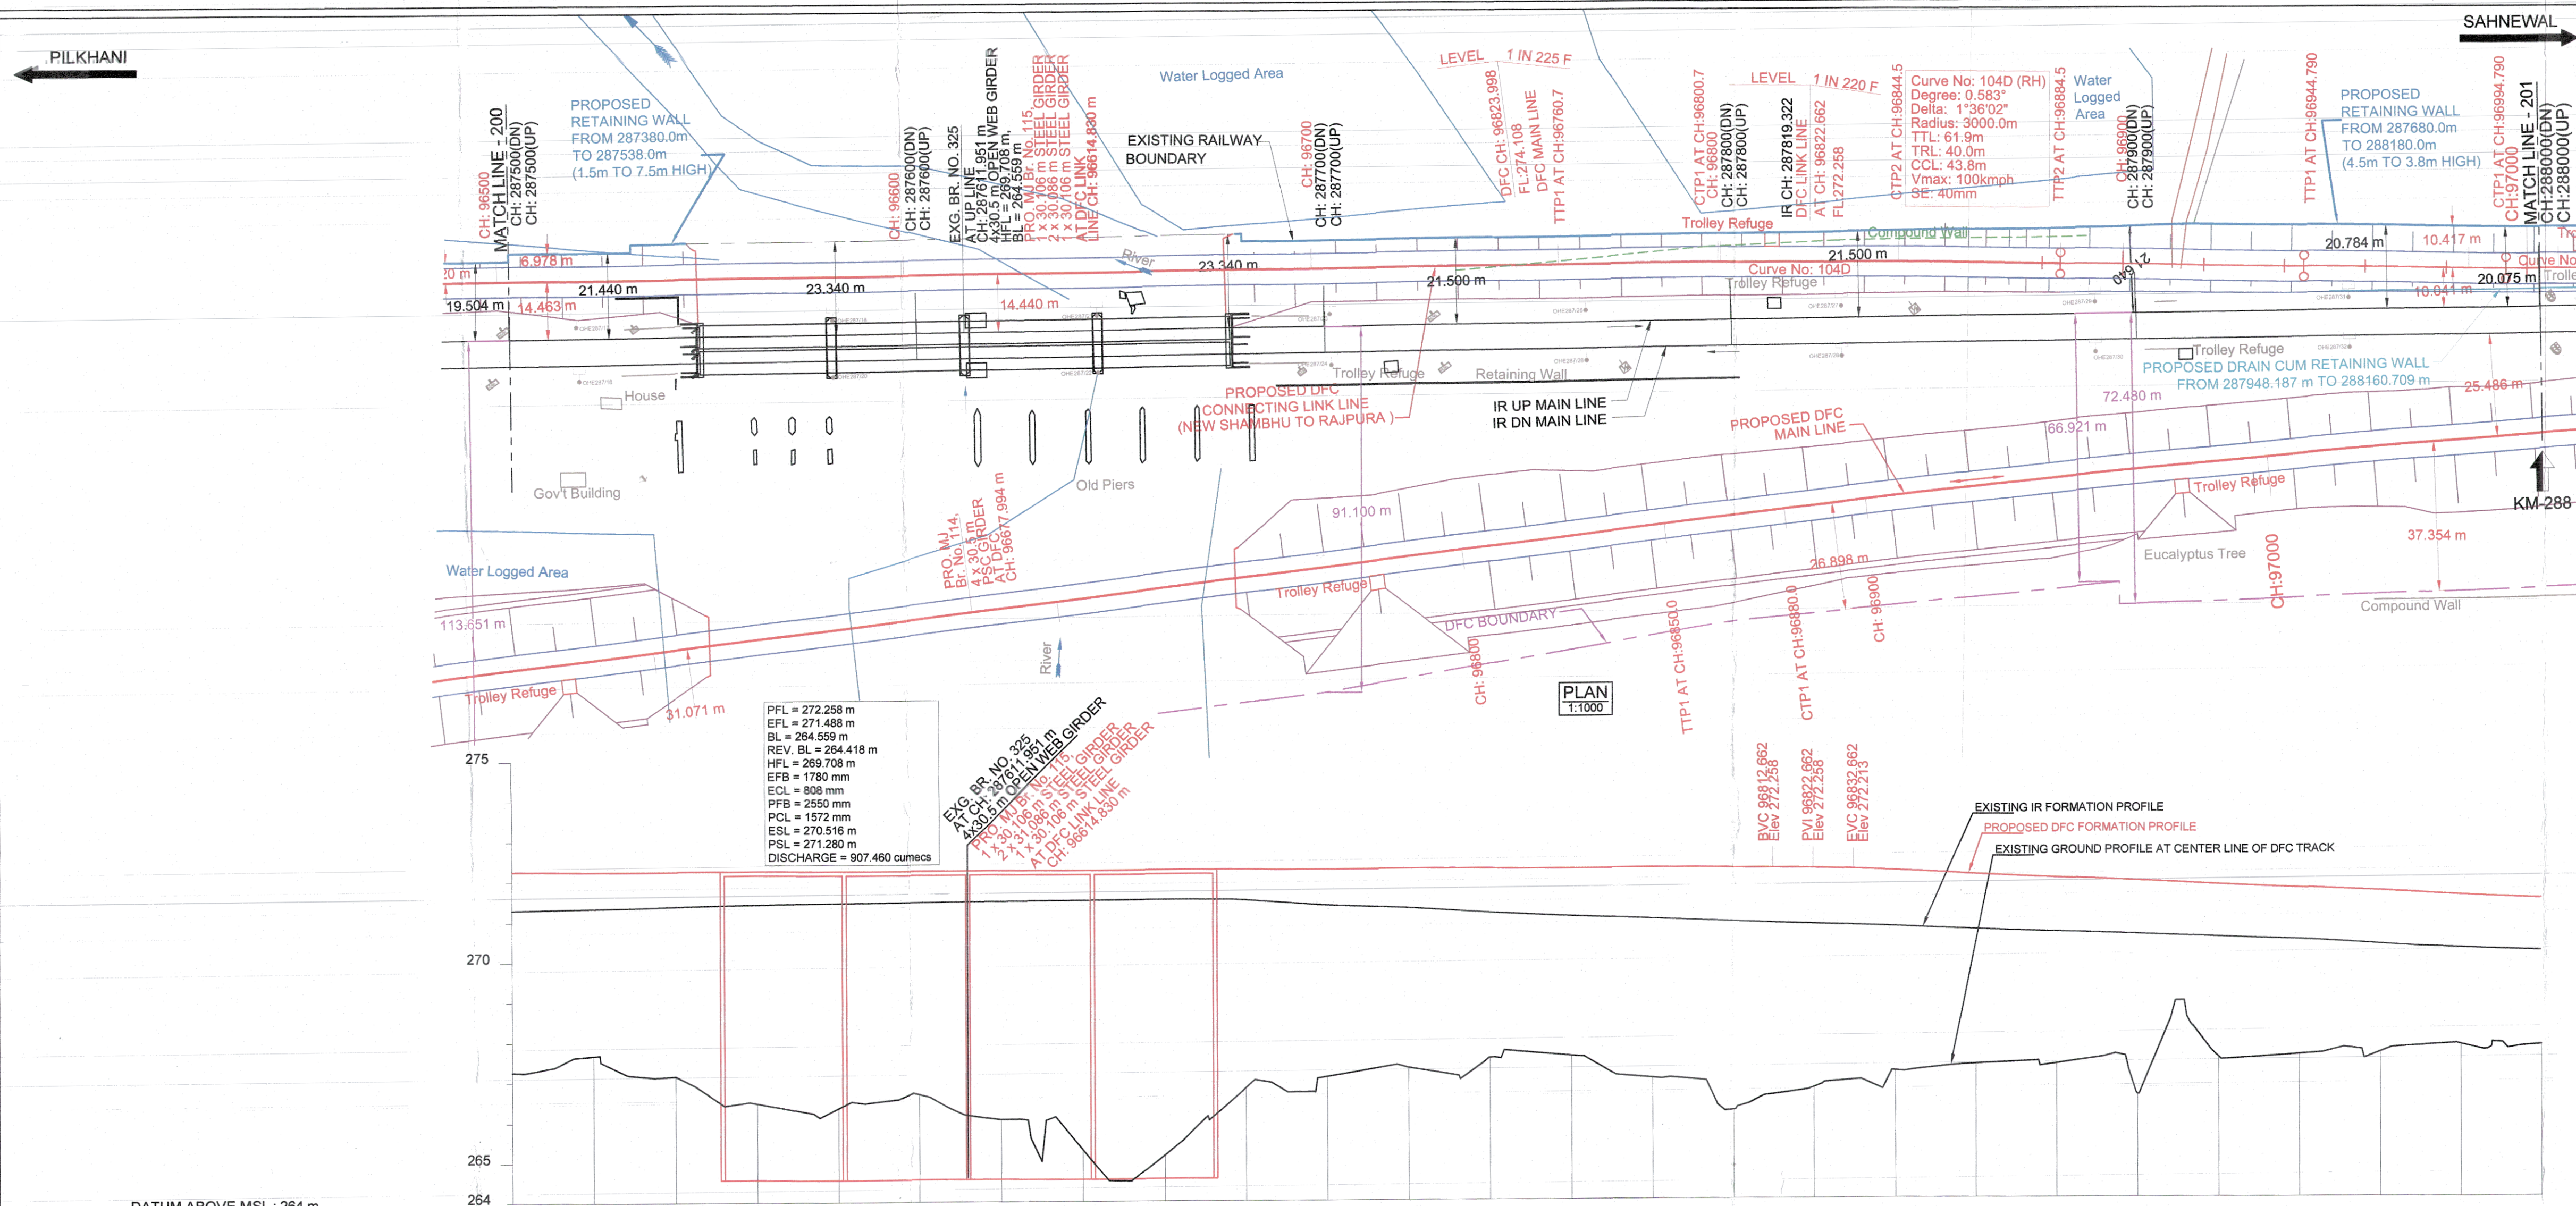

WITH NEW GTS VALUE

SHEET NO. 201A OF 346

NOTE:

- PROPOSED WORKS ARE SHOWN IN RED.
- IR PROPOSALS ARE SHOWN IN VIOLET.
- ALL DIMENSIONS ARE SHOWN IN METRES.
- THIS DRAWING IS PREPARED BASED ON LATEST SURVEY DATA HELD ON AUG-2016. GTS BENCH MARK OF 261.850 m CONSIDERED ON TOP OF CANAL BRIDGE ABUTMENT AT DORAH VILLAGE ALONG THE NH1.
- MINIMUM OF 6m TRACK CENTER MAINTAINED BETWEEN ADJACENT TRACK TO EXISTING IR TRACK IN STATION YARD PORTION.
- DFC CHAINAGE OF 5000 m IS WITH REFERENCE TO THE IR CHAINAGE OF 192.000.
- PUBLIC UTILITIES, HT, LT LINES AND OFC CABLES, WATER LINES ETC., INTERFERING DFC LINES SHALL BE RELOCATED.
- PLAN OF LONGITUDINAL AS WELL AS CROSS DRAINAGE WORKS BETWEEN IR & DFC BANKS SHALL BE SUBMITTED SEPARATELY FOR APPROVAL.
- ALL CANAL BRIDGES REQUIRED TO BE APPROVED BY CANAL AUTHORITIES.
- NECESSARY EMBANKMENT/SLOPE PROTECTION WORK DESIGN & DRAWING WILL BE SUBMITTED SEPARATELY.
- UNDERTAKING OF NO EXTRA CLAIM FOR DESIGN & EXECUTION OF WORK DUE TO CHANGE IN TURNOUT LENGTH AND DRAINAGE DESIGN HAS BEEN GIVEN BY GIL-TPL.
- DURING CENTER LINE STAKING IF GROUND LEVEL SHOWN, FOUND TO BE MAJOR VARIATION, DESIGNER TO BE INFORMED.
- THE LAND BOUNDARY SHOWN IN THE ALIGNMENT DRAWING IS TENTATIVE ONLY. FOR ACTUAL ACQUISITION REFER LAND PLANS OF THAT CORRESPONDING SECTION.
- BR. NO. 326/15 DATA PROVIDED AS PER PRELIMINARY DRAWING NO. 301-1/RB/1762 TO 301-1/RB/1764.
- LOCATIONS PRONE TO FLOODING IN THE SECTION: NO.
- WATER LOGGED AREA/ MARSHY LAND WHERE GROUND IMPROVEMENT REQUIRED: NO.
- LOCATION OF TROLLEY REFUGE SHOWN ARE INDICATIVE, WILL BE FINALISED SEPARATELY.


REFERENCE DRAWINGS:-

- FOR KEY PLAN REFER DRAWING NO. 301-2/AL/0001.
- FOR LEGEND AND ABBREVIATIONS REFER DRAWING NO. 301-2/AL/1000.
- MENTION THE ALIGNMENT OF DFC.

THIS CONSTRUCTION DRAWING OF PLAN & PROFILE IS PREPARED BASED ON PRELIMINARY DRAWING APPROVAL BY DFCCIL COMMUNICATED UNDER LETTER NO. EDC/3/PMC/CON/11/2017/0715 DATED: 20.11.2017

HORIZONTAL ALIGNMENT		L = 318.749m		TL = 40m		R = 3000m		TL = 40m		L = 60.290m		TL = 50m	
VERTICAL ALIGNMENT		L = 339.7 m		L = 20.0 m		R = 4400 m		L = 729.8 m		L = 729.8 m		L = 729.8 m	
TRACK DISTANCE FROM EXISTING NEAREST IR UP MAIN LINE TO PROPOSED DFC LINKED LINE		14.475	14.444	14.418	14.409	14.470	14.426	14.449	14.473	14.469	14.491	14.467	14.359
HEIGHT OF BANKING(+) / DEPTH OF CUTTING(-) (PFL-GL)		+4.989	+4.579	+5.095	+5.776	+5.893	+5.556	+6.187	+6.955	+7.102	+5.436	+5.165	+6.032
EXG GROUND LEVEL AT CENTER LINE OF PRO. DFC TRACK (GL)		267.269	267.679	267.163	266.482	266.365	266.702	266.071	265.303	265.156	265.544	265.871	266.226
EXG GROUND LEVEL AT TOE LOCATION OF PRO. DFC TRACK		266.639	266.396	266.094	265.579	265.325	266.391	264.809	265.700	265.164	265.538	265.842	266.246
DIFFERENCE BETWEEN PRO FORMATION LEVEL AND EXG FORMATION LEVEL (PFL-EFL)		0.965	0.916	0.872	0.833	0.802	0.780	0.763	0.747	0.744	0.766	0.886	1.342
PRO. DFC FORMATION LEVEL (PFL)		272.258	272.258	272.258	272.258	272.258	272.258	272.258	272.258	272.258	272.258	272.258	272.258
EXG. FORMATION LEVEL OF EXG IR UP MAIN LINE (EFL)		271.293	271.342	271.386	271.425	271.456	271.478	271.495	271.511	271.514	271.517	271.517	271.517
DIFFERENCE BETWEEN PRO. DFC RAIL LEVEL AND EXG. RAIL LEVEL (PRL - ERL)		1.019	0.970	0.926	0.887	0.856	0.834	0.817	0.801	0.798	0.820	0.950	1.396
PRO. DFC RAIL LEVEL (PRL)		273.000	273.000	273.000	273.000	273.000	273.000	273.000	273.000	273.000	273.000	273.000	273.000
EXG. RAIL LEVEL OF NEAREST IR UP MAIN LINE (ERL)		271.981	272.030	272.074	272.113	272.144	272.166	272.183	272.199	272.202	272.180	272.050	271.604
EQUIVALENT CHAINAGE ON PROPOSED DFC TRACK		96502.9	96522.8	96542.9	96562.9	96582.8	96602.9	96622.9	96642.9	96662.9	96682.9	96702.9	96722.9
EXISTING IR CHAINAGE		287500.0	287520.0	287540.0	287560.0	287580.0	287600.0	287620.0	287640.0	287660.0	287680.0	287700.0	287720.0

REV.	DATE	REVISION DETAILS	PURPOSE OF ISSUE
3	08.05.23	REVISED AS PER SITE CONDTION	FOR APPROVAL
2	26.03.18	UPDATED AS PER PMC COMMENTS	FOR APPROVAL
1	16.03.18	COMPLIANCE TO PMC COMMENTS, Dt. 30.12.17	FOR APPROVAL
0	13.12.17	INITIAL SUBMISSION	FOR APPROVAL

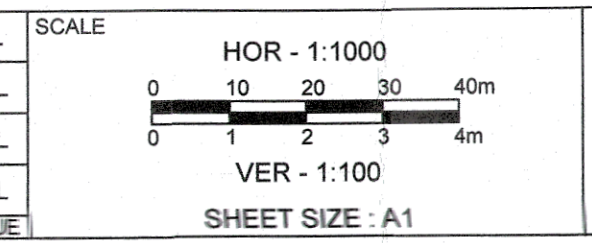

DESIGN CONSULTANT	CONTRACTOR	ENGINEER	CONTRACTOR	ENGINEER
arvee associates architects engineers & consultants pvt.ltd.	GIL - TPL JV	DB Engineering & Consulting GmbH	L.V. DUTTA DESIGNED	H.D. VIJAK NONO
			GAGANDEEP ALIGNMENT EXPERT	BABUL SAHU REVIEWED
			R.C. MISHRA TRACK HEAD	SANJAY PRASAD SINGH CPM - APPROVED

TRACK STRUCTURE		
RAIL SECTION: 60Kg/m (UIC 60Kg/m) DFC LINE: 60Kg/m (UIC 60Kg/m) IR MAIN LINE: 52Kg/m		Difference between FL and RL
	IR Line	DFC
RUBBER PAD	172mm	172mm
SLEEPER DEPTH	6mm	10mm
BALLAST CUSHION	210mm	210mm
	300mm	350mm
Total Depth (FL TO RL)	688mm	742mm

PROJECT OFFICE / DFCCIL		
PANKAJ KUMAR GUPTA CGM		
YOGESH KUMAR GM / ELECT. / UMB		
SANDEEP KUMAR PM / ENGG-1 / UMB	S.P. SHARMA PM / ELECT. / UMB	MOZAHIR ANWAR PM / S&T / UMB
SRIKANT VERMA JPM / ENGG-1 / UMB	GURMEET SINGH DPM / ELECT. / UMB	DEBASISH NAYAK DPM / S&T / UMB

OWNER	DEDICATED FREIGHT CORRIDOR CORPORATION OF INDIA LTD. (A GOVERNMENT OF INDIA ENTERPRISE) PROJECT OFFICE (AMBALA UNIT): OLD RAILWAY COLONY (NEAR ANAND MARKET), AMBALA CANTT-133001. CORPORATE IDENTITY NO.: U80232DL20060501155068
PROJECT	EASTERN DEDICATED FREIGHT CORRIDOR SAHNEWAL TO PILKHANI CONTRACT PACKAGE - 301

TITLE	PLAN & PROFILE FROM IR KM: 287.500 TO 288.000 FROM DFC KM: 96.003 TO 96.503 (CONNECTING LINK LINE)
DFCC APPR. NO. -	ENGG. APPR. NO. -
DRG. NO. - 301-2/AL/1201A	REVISION NO. -
SHEET NO. : 201A OF 346	DATE: 08.05.2023
3	D