




PILKHANI

SAHNEWAL

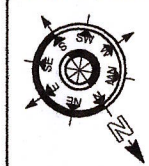

WITH NEW GTS VALUE

SHEET NO. 204A OF 346

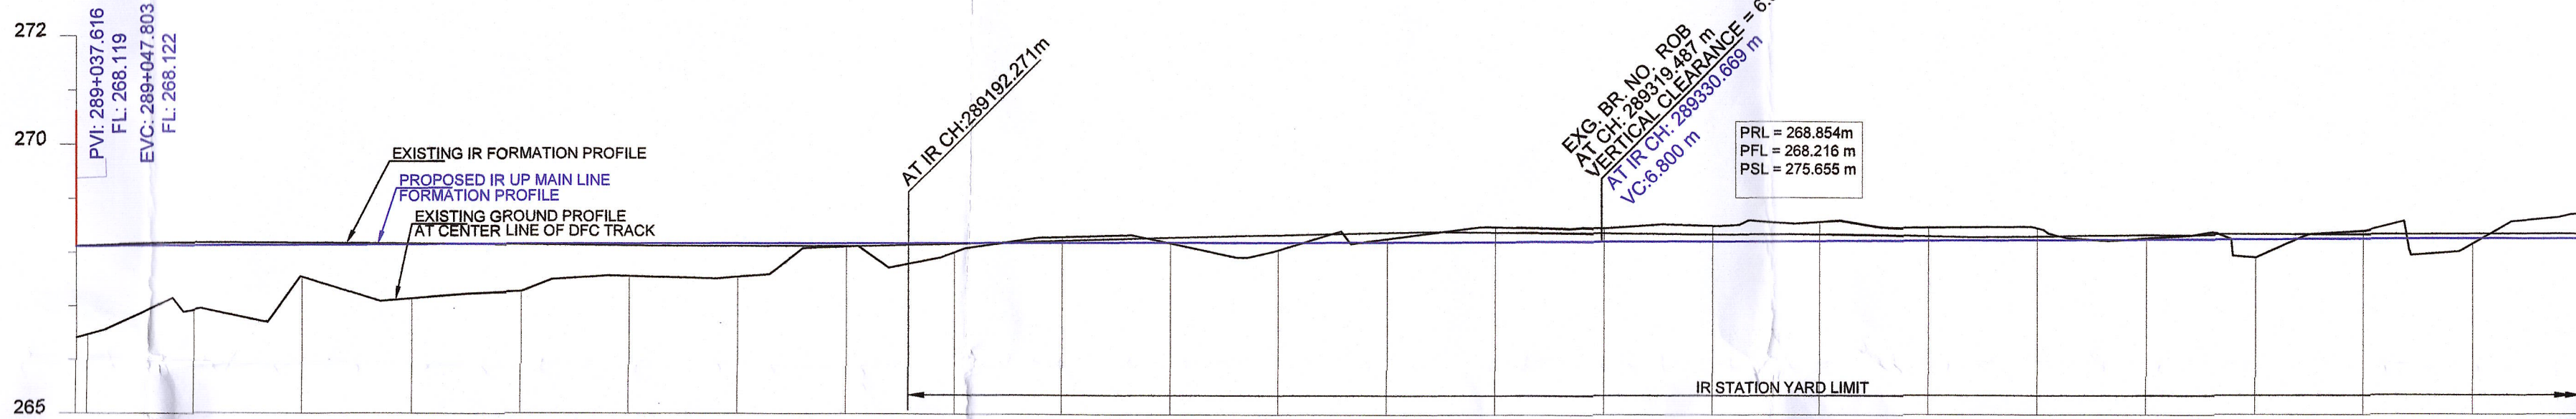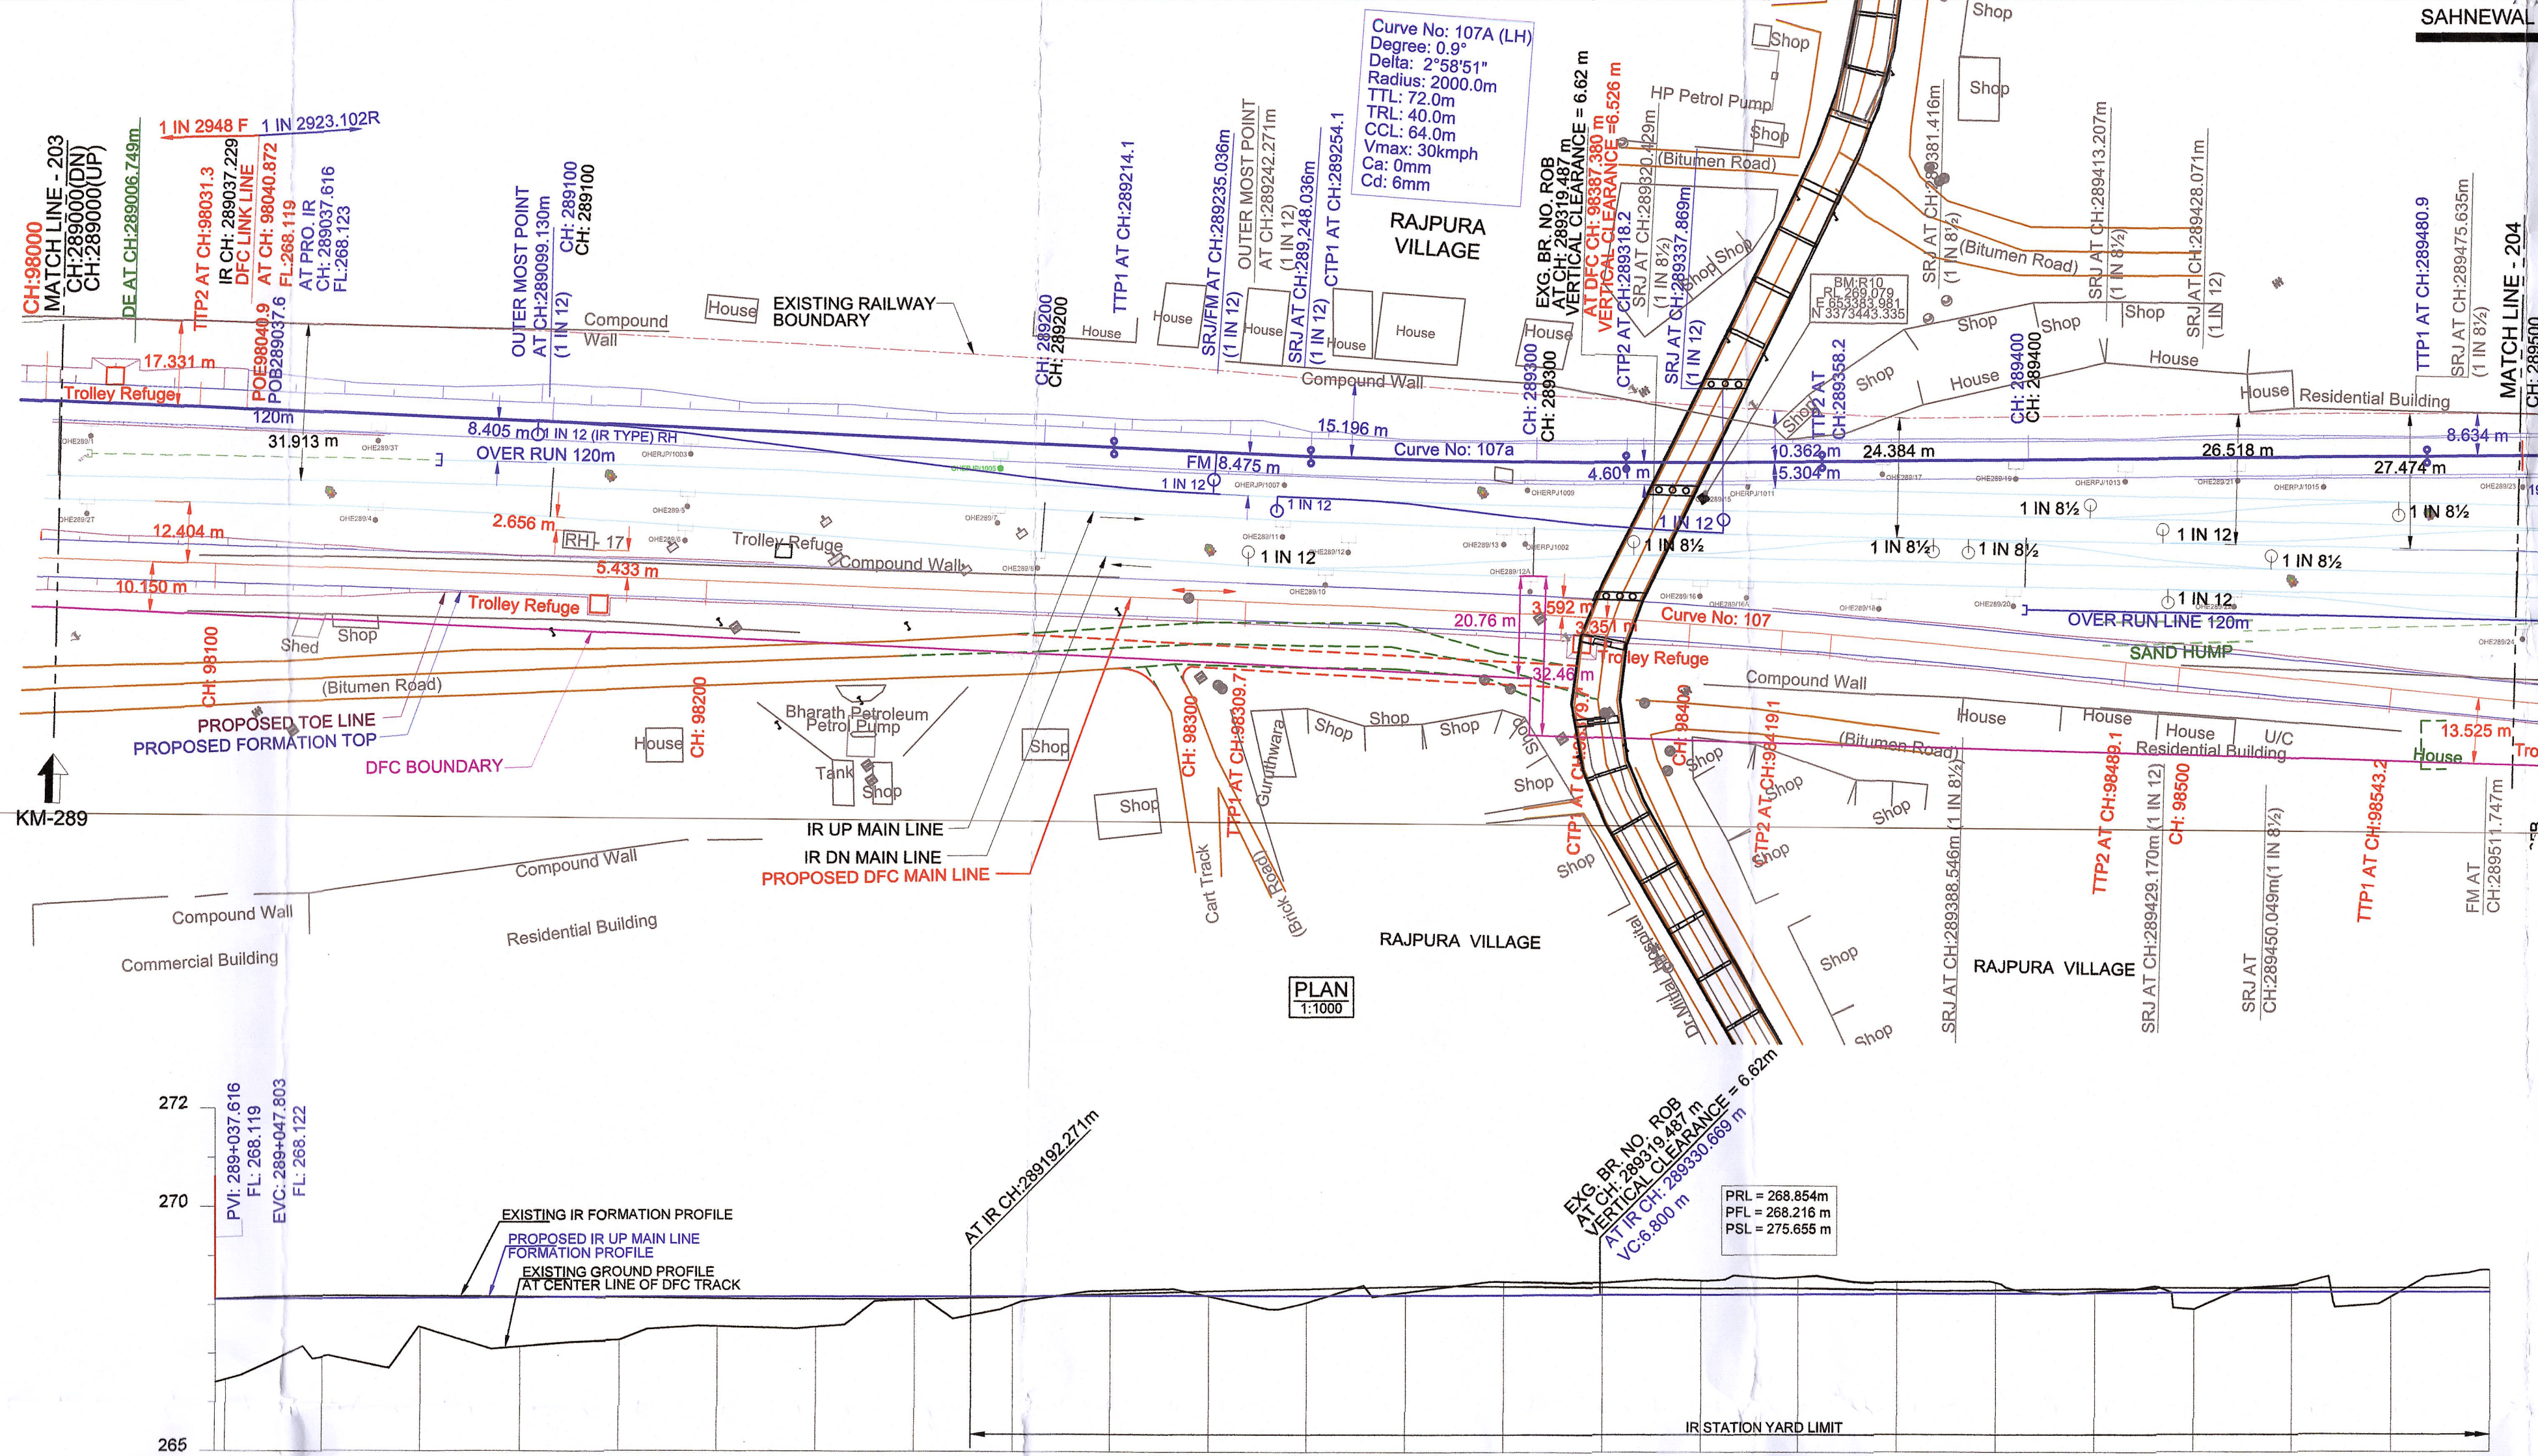

DATUM ABOVE MSL : 265 m

HORIZONTAL ALIGNMENT	SL=186.099m	TRL=40.000	CCL=64.048 R=2000	TRL=40.000	SL=122.704m	TRL=30.000
VERTICAL ALIGNMENT	L=20.374m R=69555.02				G=1:2923.102 L=545.654m	
TRACK DISTANCE FROM EXISTING NEAREST IR UP MAIN LINE TO PROPOSED IR UP MAIN LINE	14.236 14.191					
HEIGHT OF BANKING(+) / DEPTH OF CUTTING(-) (PFL-GL)	1.704 1.646					
EXG GROUND LEVEL AT CENTER LINE OF PRO. IR TRACK (GL)	268.415 268.415					
EXG GROUND LEVEL AT TOE LOCATION OF PRO. IR TRACK	268.415 268.415					
DIFFERENCE BETWEEN PRO IR FORMATION LEVEL AND EXG. IR FORMATION LEVEL (PFL-EFL)	-0.000 -0.000					
PRO. IR FORMATION LEVEL (PFL)	268.119 268.120					
EXG. FORMATION LEVEL OF EXG IR UP MAIN LINE (EFL)	268.123 268.129					
DIFFERENCE BETWEEN PRO. IR RAIL LEVEL AND EXG. RAIL LEVEL (PRL - ERL)	0.054 0.053					
PRO. IR RAIL LEVEL (PRL)	268.811 268.817					
EXG. RAIL LEVEL OF NEAREST IR UP MAIN LINE (ERL)	268.811 268.817					
EQUIVALENT CHAINAGE ON PROPOSED IR UP TRACK	289037.9 289040.0					
EXISTING IR CHAINAGE	289037.9 289040.0					

L - SECTION (CONNECTING LINE)

REV.	DATE	REVISION DETAILS	PURPOSE OF ISSUE
3	17.08.23	MODIFICATION OF TRACK ALIGNMENT OF LOOP LINE AS PER PMC-LTR NO. PMCE/FC301/PMC/CON/07/2023/9407	FOR APPROVAL
2	26.03.18	UPDATED AS PER PMC COMMENTS	FOR APPROVAL
1	16.03.18	COMPLIANCE TO PMC COMMENTS, DL 30.12.17	FOR APPROVAL
0	13.12.17	INITIAL SUBMISSION	FOR APPROVAL

SCALE

HOR - 1:1000

VER - 1:100

SHEET SIZE : A1

DESIGN CONSULTANT














CONTRACTOR



ENGINEER



CONTRACTOR

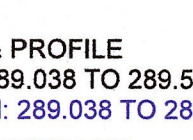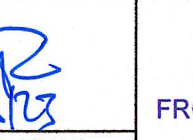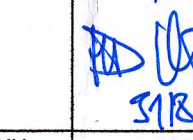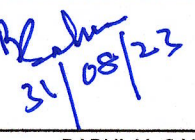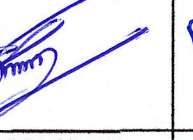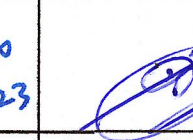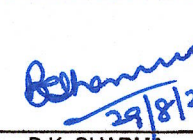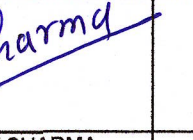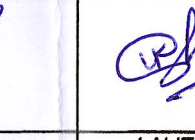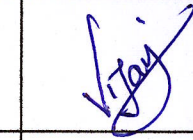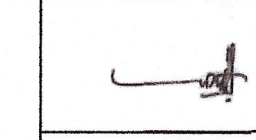

TRACK STRUCTURE		
RAIL SECTION: 60Kg/m (UIC 60Kg/m) DFC LINE: 60Kg/m (UIC 60Kg/m)	Difference between FL and RL	
	IR Line	DFC
RUBBER PAD	172mm	172mm
SLEEPER DEPTH	6mm	10mm
BALLAST CUSHION	210mm	210mm
	250mm	350mm
Total Depth (FL TO RL)	638mm	742mm

PROJECT OFFICE / DFCCL

PANKAJ KUMAR GUPTA

CSM

06.09.2023

YOGESH KUMAR

GM / ELECT. / UMB

SANDEEP KUMAR

PM / ENGG-1 / UMB

S.P. SHARMA

PM / ELECT. / UMB

MOZAHIR ANWAR

PM / S&T / UMB

SRIKANT VERMA

JPM / ENGG-1 / UMB

GURMEET SINGH

DPM / ELECT. / UMB

DEBASISH NAYAK

DPM / S&T / UMB

GOOD FOR CONSTRUCTION

OWNER



DEDICATED FREIGHT CORRIDOR CORPORATION OF INDIA LTD.
(A GOVERNMENT OF INDIA ENTERPRISE)
PROJECT OFFICE (AMBALA UNIT): OLD RAILWAY COLONY (NEAR ANAND MARKET), AMBALA CANTT-133001.
CORPORATE IDENTITY NO. : U60232DL2006G01155068

PROJECT

EASTERN DEDICATED FREIGHT CORRIDOR
SAHNEWAL TO PILKHANI
CONTRACT PACKAGE - 301

TITLE

PLAN & PROFILE
FROM IR KM: 289.038 TO 289.500
FROM PRO. IR KM: 289.038 TO 289.500
(CONNECTING LINE)

DFCC APPR. NO. -

ENGG. APPR. NO. -

DRG. NO. - 301-2/AL/1204A

SHEET NO. : 204A OF 346

DATE : 17.08.23

REV. No.

3

STATUS

GC