


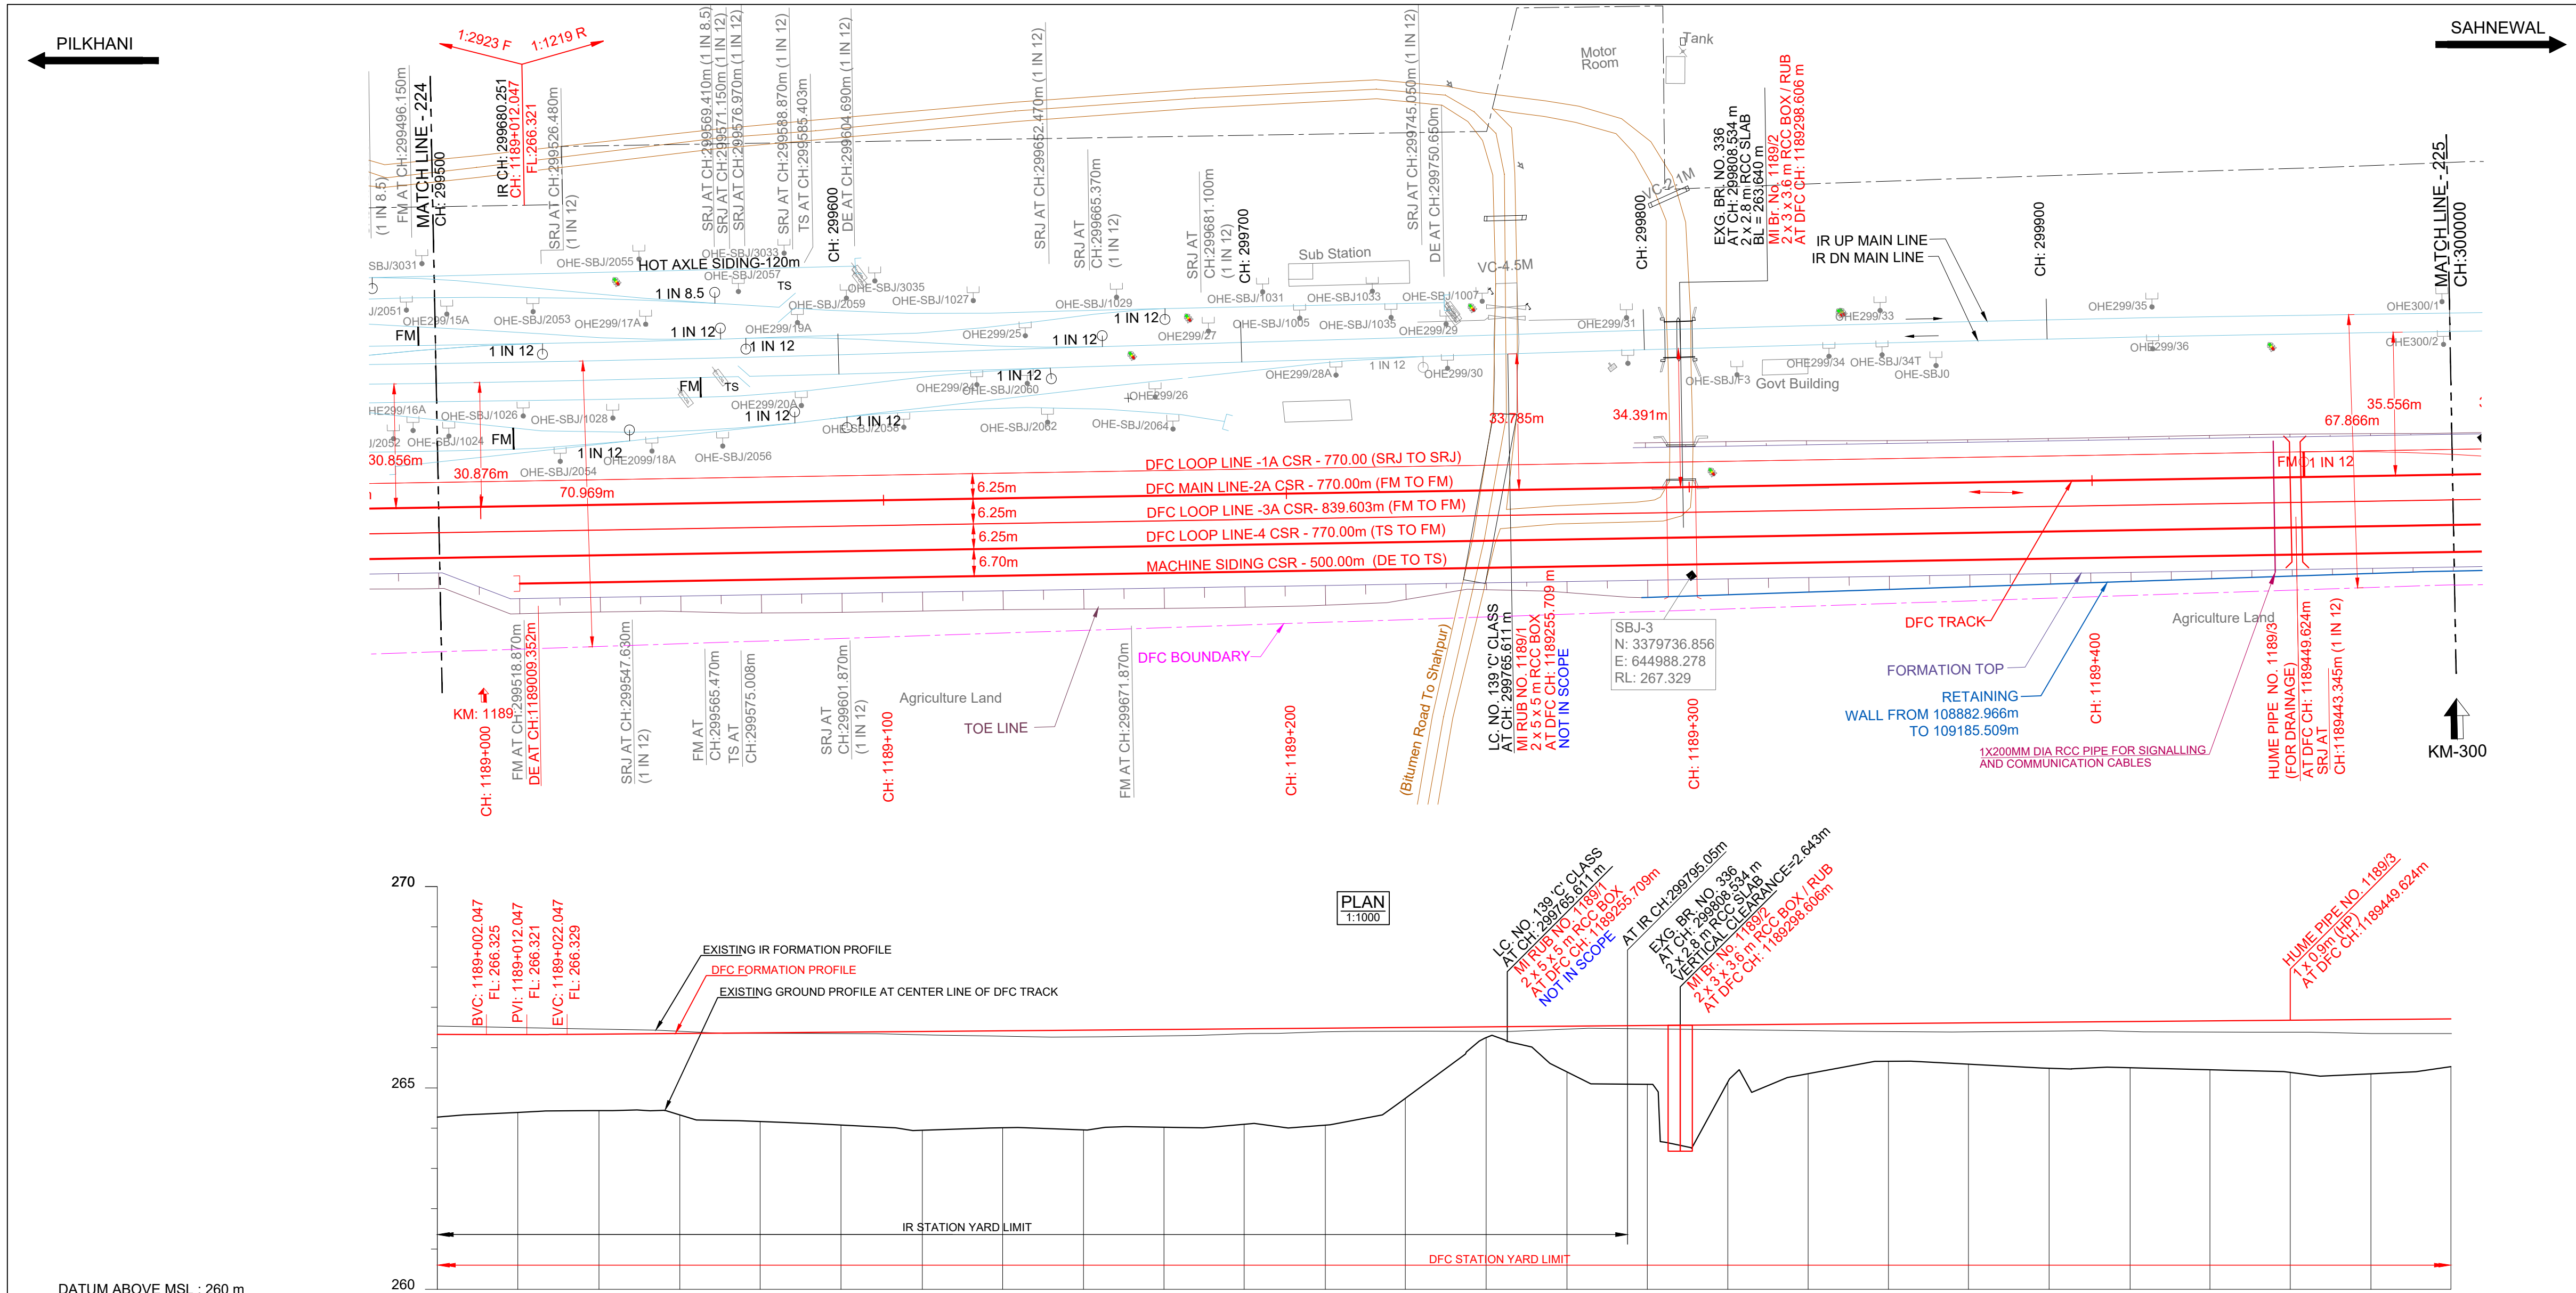

HORIZONTAL ALIGNMENT	L = 1484.776m	
VERTICAL ALIGNMENT	L = 1107.832 m 1 IN 1219.493 R	
TRACK DISTANCE FROM EXISTING NEAREST IR DN MAIN LINE TO DFC MAIN LINE	30.848	30.910
HEIGHT OF BANKING(+) / DEPTH OF CUTTING(-) (PFL-GL)	+2.055	+1.935
EXG GROUND LEVEL AT CENTER LINE OF DFC TRACK (GL)	264.274	264.330
EXG GROUND LEVEL AT TOE LOCATION OF DFC TRACK	264.303	264.304
DIFFERENCE BETWEEN DFC FORMATION LEVEL AND EXG.FORMATION LEVEL.(PFL-EFL)	-0.206	-0.173
DFC FORMATION LEVEL (PFL)	266.329	266.324
EXG. FORMATION LEVEL OF EXG IR DN MAIN LINE (EFL)	266.535	266.497
DIFFERENCE BETWEEN DFC RAIL LEVEL AND EXG. RAIL LEVEL (PRL - ERL)	0.165	0.134
DFC RAIL LEVEL (PRL)	267.042	267.035
EXG.RAIL LEVEL OF NEAREST IR DN MAIN LINE(ERL)	267.207	267.169
EQUIVALENT CHAINAGE ON DFC TRACK	2995000.0	2995200.0
EXISTING IR CHAINAGE	2995000.0	2995200.0

L - SECTION