


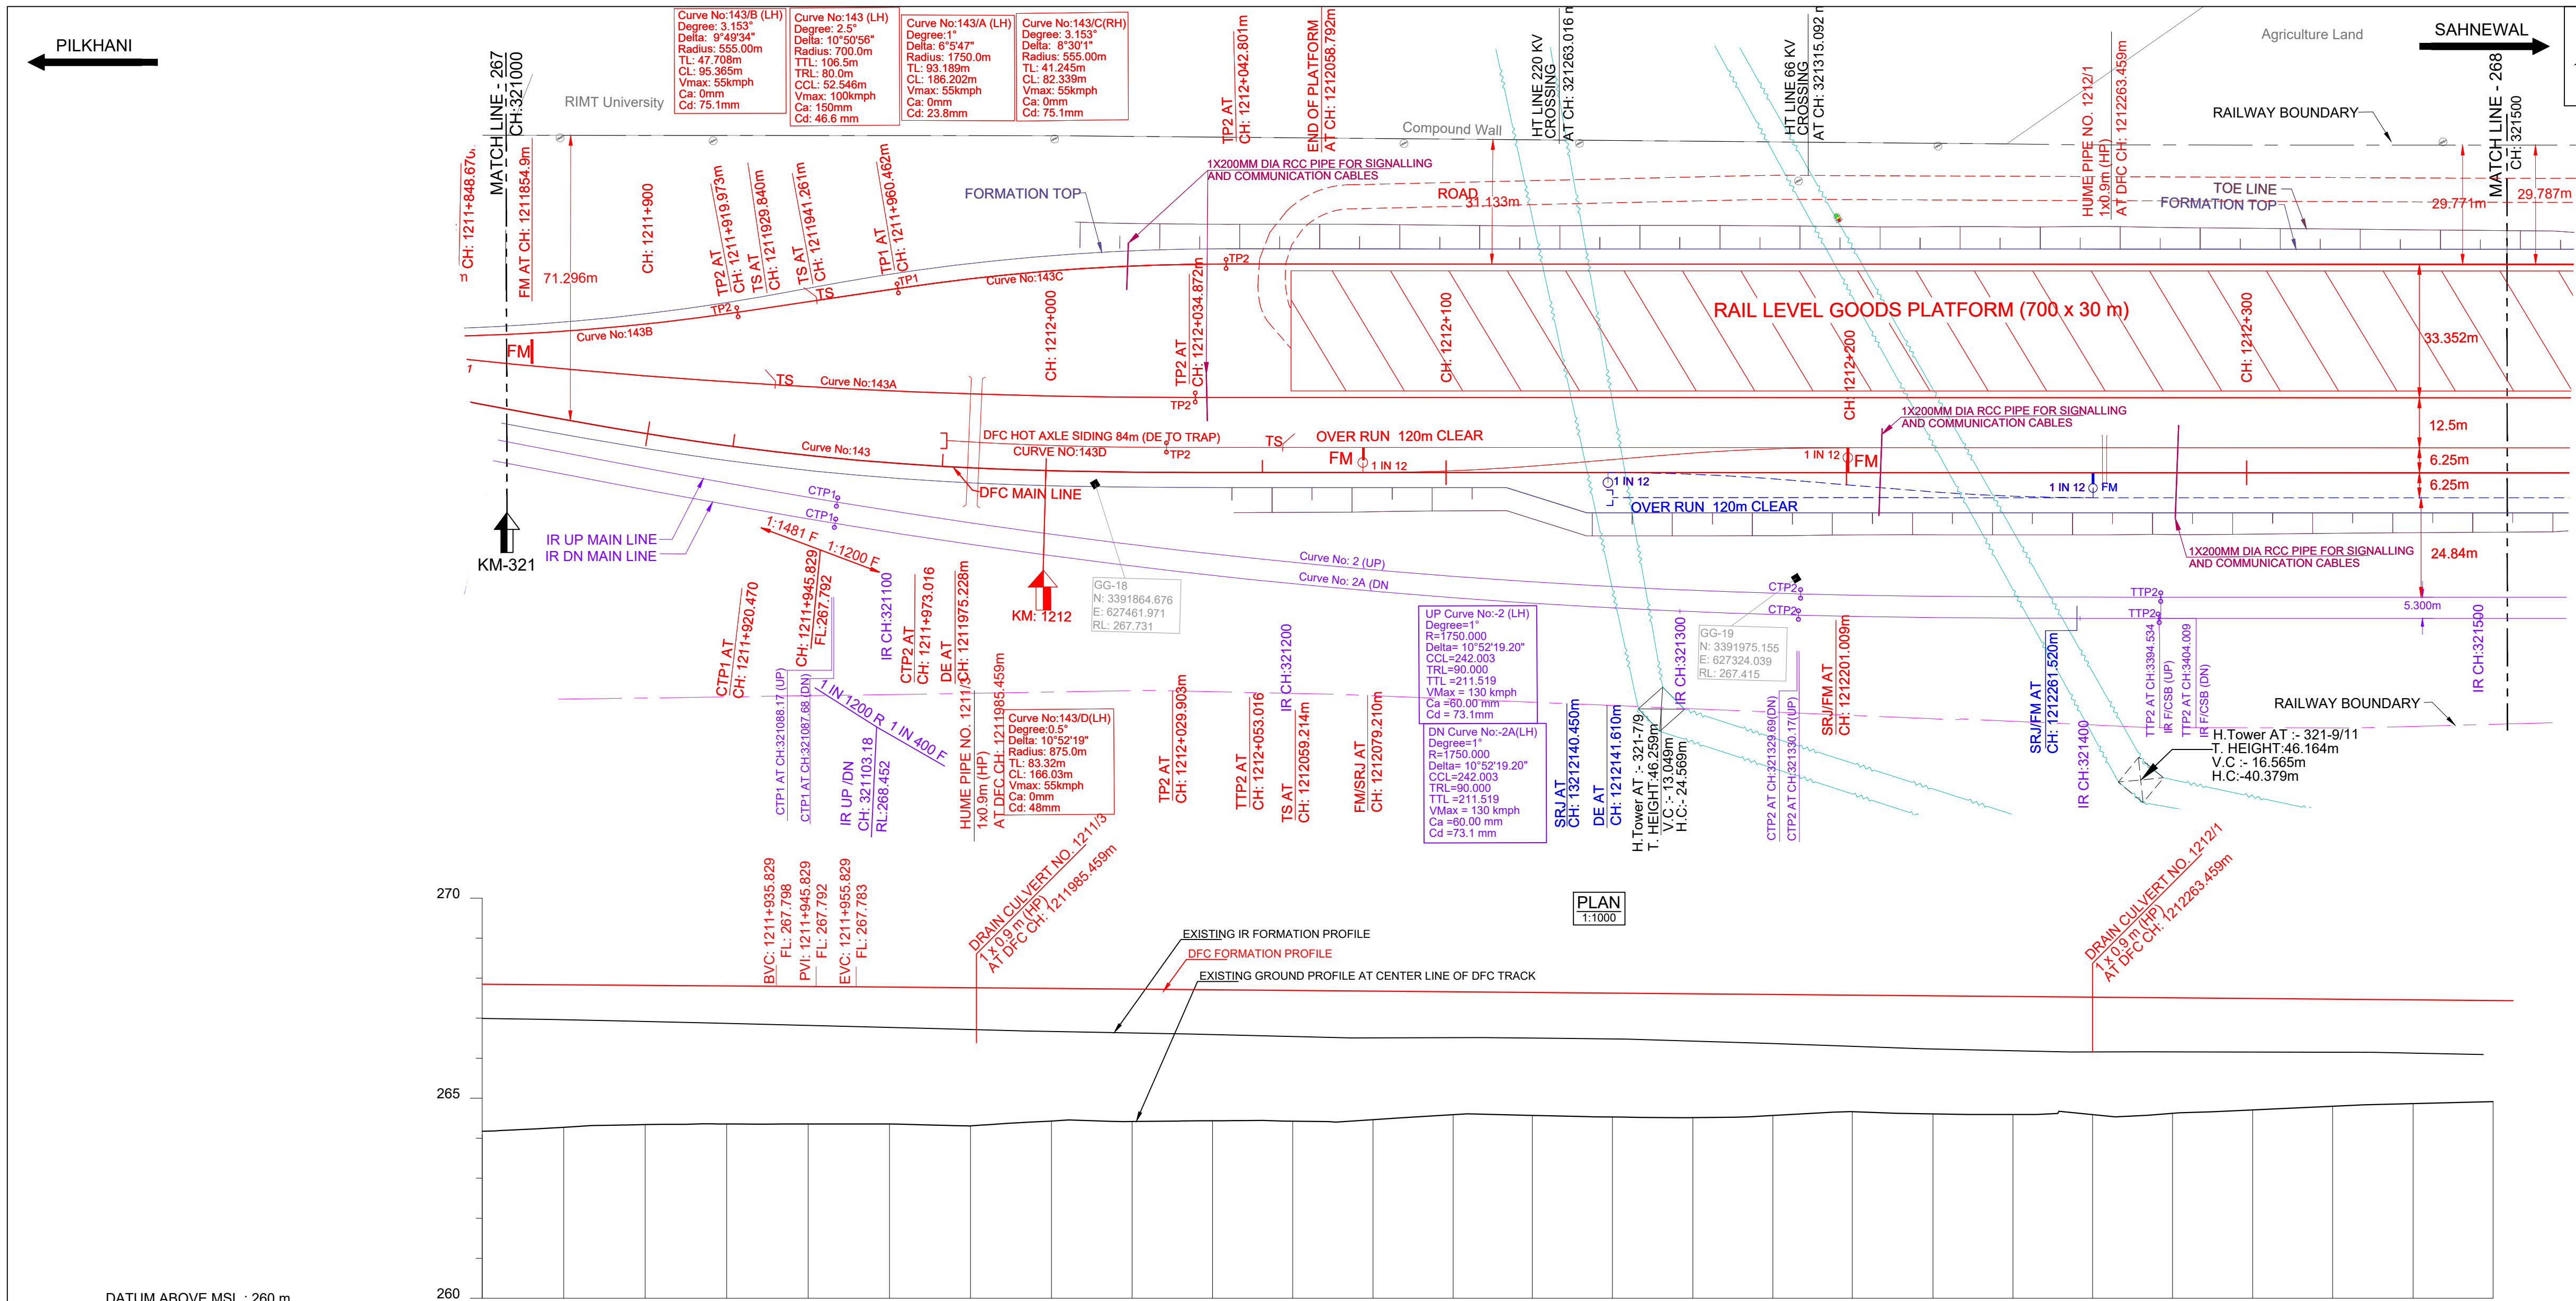

HORIZONTAL ALIGNMENT	TL= 80m R =700m TL= 80m L = 2464.208m																							
VERTICAL ALIGNMENT	L=346.294 m 1 IN 1481.173 F L=20.0 m R=126428 m L=1915.351 m 1 IN 1200 F																							
TRACK DISTANCE FROM EXISTING NEAREST IR UP MAIN LINE TO DFC MAIN LINE	44.628	48.263	51.582	54.430	56.705	58.402	59.528	60.168	60.474	60.575	60.627	60.681	60.753	60.787	60.789	60.815	60.851	60.837	60.816	60.846	60.836	60.835	60.853	
HEIGHT OF BANKING(+) / DEPTH OF CUTTING(-) (PFL-GL)	+3.674	+3.561	+3.480	+3.451	+3.438	+3.420	+3.451	+3.321	+3.310	+3.275	+3.268	+3.222	+3.081	+3.073	+3.095	+3.096	+3.032	+2.916	+2.951	+2.951	+2.684	+2.598	+2.532	
EXG GROUND LEVEL AT CENTER LINE OF DFC TRACK (GL)	264.158	264.273	264.340	264.356	264.355	264.357	264.309	264.423	264.417	264.435	264.425	264.455	264.579	264.571	264.532	264.514	264.562	264.661	264.609	264.593	264.793	264.882	264.912	
EXG GROUND LEVEL AT TOE LOCATION OF DFC TRACK	264.158	264.273	264.340	264.356	264.355	264.357	264.309	264.423	264.417	264.435	264.425	264.455	264.579	264.571	264.532	264.514	264.562	264.661	264.609	264.593	264.793	264.882	264.912	
DIFFERENCE BETWEEN DFC FORMATION LEVEL AND EXG.FORMATION LEVEL (PFL-EFL)	-0.855	-0.872	-0.902	-0.934	-0.971	-1.005	-1.038	-1.072	-1.092	-1.114	-1.147	-1.172	-1.148	-1.114	-1.144	-1.175	-1.220	-1.273	-1.327	-1.354	-1.342	-1.330	-1.351	
DFC FORMATION LEVEL (PFL)	267.848	267.834	267.820	267.807	267.793	267.777	267.760	267.744	267.727	267.710	267.693	267.677	267.660	267.644	267.627	267.610	267.594	267.577	267.560	267.510	267.477	267.444	267.444	
EXG. FORMATION LEVEL OF EXG IR UP MAIN LINE (EFL)	-266.993	-266.962	-266.918	-266.873	-266.822	-266.772	-266.722	-266.672	-266.635	-266.596	-266.546	-266.505	-266.512	-266.504	-266.483	-266.435	-266.374	-266.304	-266.233	-266.156	-266.152	-266.093	-266.093	
DIFFERENCE BETWEEN DFC RAIL LEVEL AND EXG. RAIL LEVEL (PRL - ERL)	0.896	0.913	0.943	0.975	1.012	1.046	1.080	1.112	1.133	1.156	1.188	1.212	1.189	1.180	1.185	1.217	1.260	1.314	1.368	1.395	1.371	1.371	1.391	
DFC RAIL LEVEL (PRL)	268.561	268.547	268.533	268.520	268.506	268.490	268.473	268.457	268.440	268.423	268.406	268.390	268.373	268.357	268.340	268.323	268.307	268.290	268.273	268.223	268.190	268.173	268.157	
EXG.RAIL LEVEL OF NEAREST IR UP MAIN LINE(ERL)	267.665	267.634	267.590	267.545	267.494	267.444	267.394	267.344	267.307	267.268	267.218	267.177	267.184	267.176	267.155	267.107	267.046	266.976	266.905	266.828	266.819	266.802	266.765	
EQUIVALENT CHAINAGE ON DFC TRACK	-1211863.1	-1211863.2	-1211903.5	-1211923.7	-1211943.8	-1211963.9	-1211983.9	-1212004.0	-1212024.0	-1212044.1	-1212064.1	-1212084.1	-1212104.1	-1212123.9	-1212143.9	-1212164.0	-1212184.0	-1212203.8	-1212224.0	-1212283.9	-1212283.9	-1212344.0	-1212384.0	
EXISTING IR CHAINAGE	321000.0	321020.0	321040.0	321060.0	321080.0	321100.0	321120.0	321140.0	321160.0	321180.0	321200.0	321220.0	321240.0	321260.0	321280.0	321300.0	321320.0	321340.0	321360.0	321380.0	321400.0	321420.0	321480.0	321500.0