


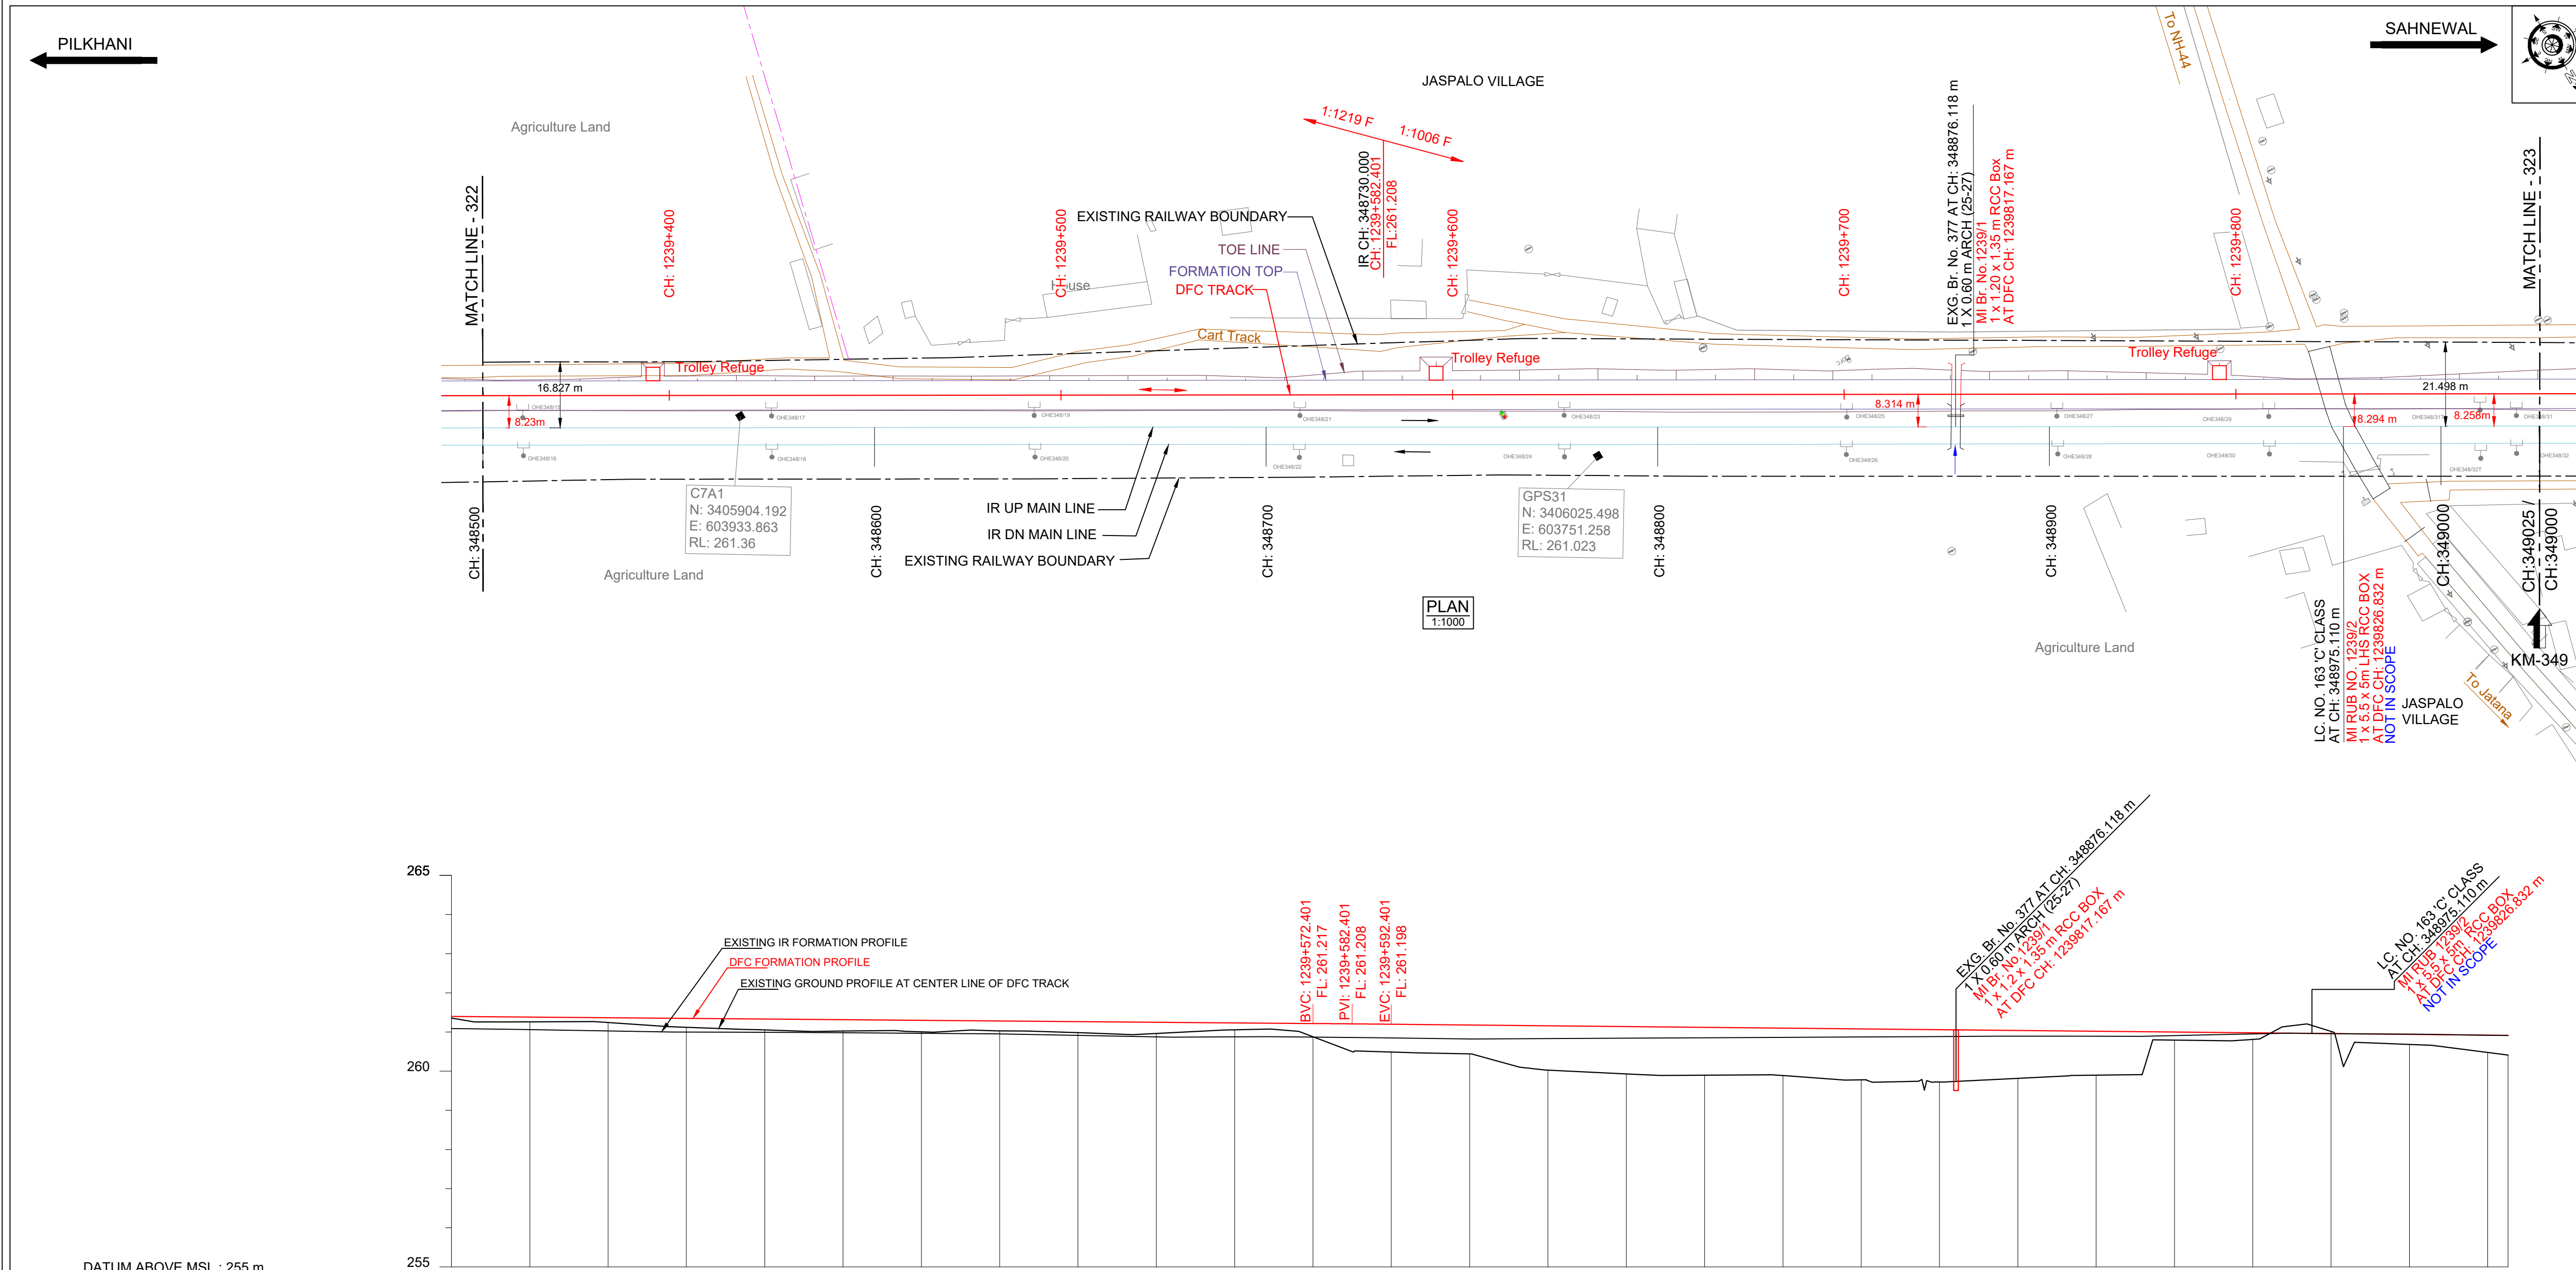

HORIZONTAL ALIGNMENT	L = 4280.337m																			
VERTICAL ALIGNMENT	L=2484.775 m 1 IN 1219.242 F L=20.0 m R=115033m L=1612.829 m 1 IN 1005.990 F																			
TRACK DISTANCE FROM EXISTING NEAREST IR UP MAIN LINE TO DFC MAIN LINE	8.233	8.227	8.242	8.249	8.235	8.224	8.214	8.204	8.196	8.188	8.221	8.250	8.269	8.288	8.297	8.306	8.315	8.324	8.329	8.307
HEIGHT OF BANKING(+) / DEPTH OF CUTTING(-) (PFL-GL)	+0.044	+0.123	+0.122	+0.228	+0.278	+0.288	+0.293	+0.255	+0.283	+0.287	+0.176	+0.340	+0.710	+0.738	+1.131	+1.210	+1.222	+1.210	+1.301	+1.338
EXG GROUND LEVEL AT CENTER LINE OF DFC TRACK (GL)	-261.353	-261.258	-261.242	-261.120	-261.053	-261.027	-261.006	-261.027	-260.983	-260.982	-261.057	-260.877	-260.488	-260.441	-260.028	-259.929	-259.897	-259.886	-260.795	-260.811
EXG GROUND LEVEL AT TOE LOCATION OF DFC TRACK	-261.137	-261.107	-260.744	-260.565	-260.638	-260.604	-260.629	-260.584	-260.554	-260.441	-260.801	-260.132	-259.916	-259.783	-259.552	-259.801	-259.315	-259.862	-260.179	-260.773
DIFFERENCE BETWEEN DFC FORMATION LEVEL AND EXG.FORMATION LEVEL (PFL-EFL)	0.308	0.320	0.336	0.351	0.339	0.333	0.333	0.331	0.352	0.373	0.356	0.349	0.352	0.359	0.329	0.298	0.268	0.237	0.092	0.030
DFC FORMATION LEVEL (PFL)	-261.397	-261.381	-261.364	-261.348	-261.331	-261.315	-261.299	-261.282	-261.266	-261.249	-261.233	-261.217	-261.198	-261.179	-261.159	-261.139	-261.119	-261.099	-261.020	-260.980
EXG. FORMATION LEVEL OF EXG IR UP MAIN LINE (EFL)	-261.089	-261.061	-261.028	-260.997	-260.992	-260.982	-260.966	-260.951	-260.914	-260.876	-260.877	-260.868	-260.846	-260.820	-260.830	-260.841	-260.851	-260.862	-260.908	-260.950
DIFFERENCE BETWEEN DFC RAIL LEVEL AND EXG. RAIL LEVEL (PRL - ERL)	0.350	0.362	0.378	0.392	0.382	0.375	0.374	0.373	0.394	0.415	0.398	0.390	0.393	0.400	0.370	0.339	0.309	0.278	0.133	0.071
DFC RAIL LEVEL (PRL)	-262.111	-262.094	-262.078	-262.062	-262.045	-262.029	-262.012	-261.996	-261.980	-261.963	-261.947	-261.930	-261.912	-261.892	-261.872	-261.852	-261.832	-261.812	-261.713	-261.693
EXG.RAIL LEVEL OF NEAREST IR UP MAIN LINE(ERL)	-261.761	-261.733	-261.700	-261.669	-261.664	-261.654	-261.638	-261.623	-261.586	-261.548	-261.549	-261.540	-261.518	-261.492	-261.502	-261.513	-261.523	-261.534	-261.580	-261.630
EQUIVALENT CHAINAGE ON DFC TRACK	-1239351.7	-1239371.7	-1239391.7	-1239411.7	-1239431.7	-1239451.7	-1239471.7	-1239491.7	-1239511.7	-1239531.7	-1239551.7	-1239571.7	-1239591.7	-1239611.7	-1239631.7	-1239651.7	-1239671.7	-1239691.7	-1239711.7	-1239731.7
EXISTING IR CHAINAGE	348500.0	348520.0	348540.0	348560.0	348580.0	348600.0	348620.0	348640.0	348660.0	348680.0	348700.0	348720.0	348740.0	348760.0	348780.0	348800.0	348820.0	348840.0	348860.0	348880.0