


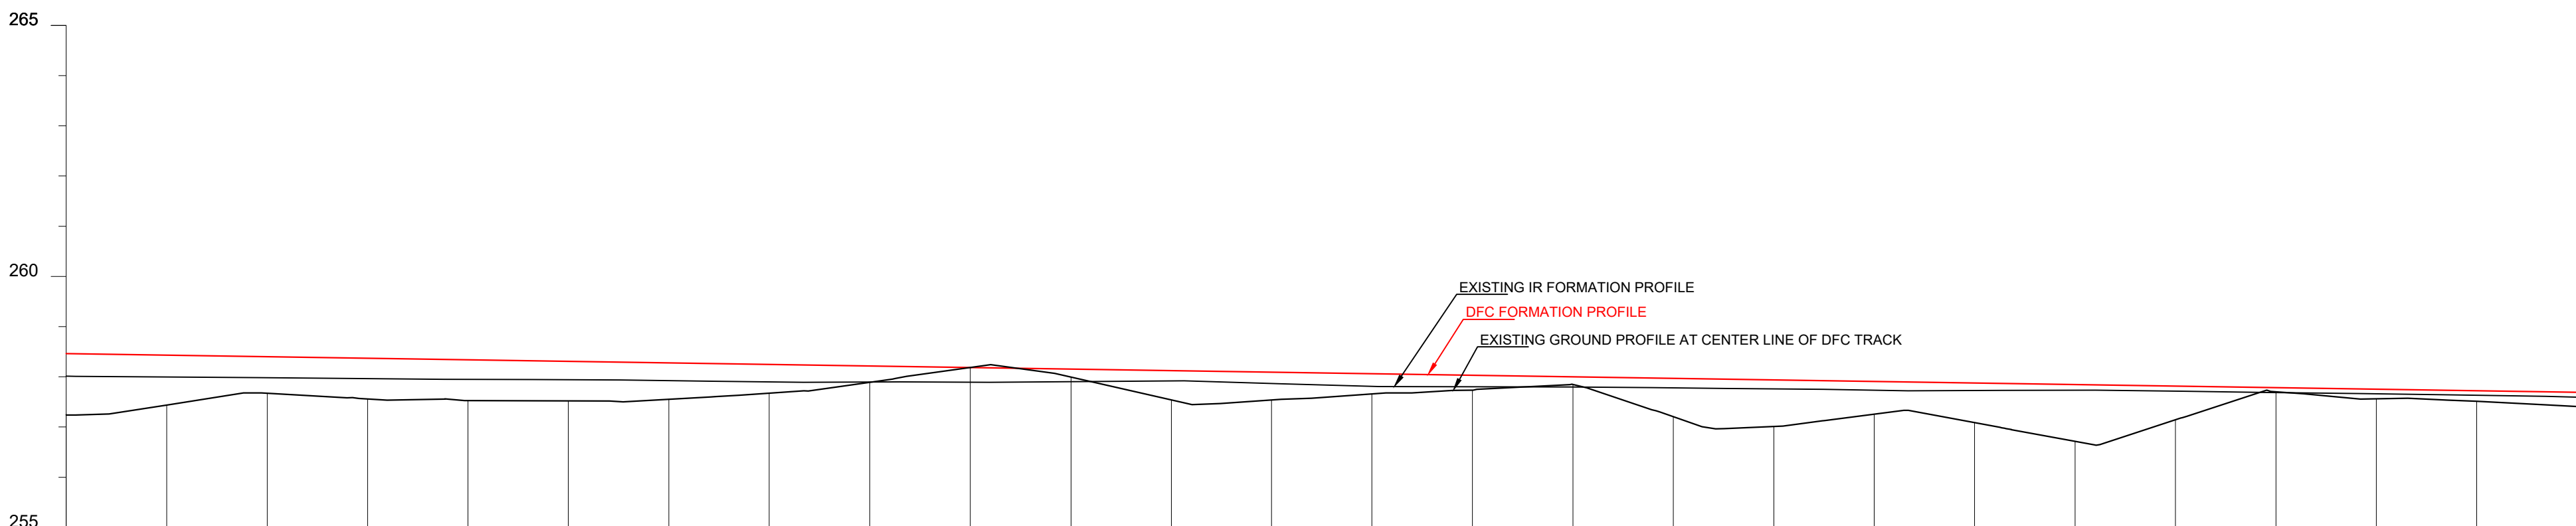

HORIZONTAL ALIGNMENT	L = 5018.785m																															
VERTICAL ALIGNMENT	L=1479.855m 1 IN 646.028 F																															
TRACK DISTANCE FROM EXISTING NEAREST IR UP MAIN LINE TO DFC MAIN LINE	8.846	8.846	8.808	8.778	8.816	8.834	8.789	8.752	8.724	8.699	8.699	8.943	8.906	8.890	8.875	8.895	8.921	8.956	8.968	8.967	8.947	8.923	8.921	8.919	8.914							
HEIGHT OF BANKING(+) / DEPTH OF CUTTING(-) (PFL-GL)	+1.222		+0.894	+0.730	+0.811	+0.814	+0.787		+0.573	+0.825	+0.825	+0.553	+0.401		+0.153		+0.328		+0.651		+0.787		+0.129		+0.071		+0.080		+0.190		+0.210	+0.284
EXG GROUND LEVEL AT CENTER LINE OF DFC TRACK (GL)	-257.242	-257.242	-257.439	-257.672	-257.560	-257.526	-257.522	-257.553	-257.674	-257.881	-257.881	-257.540	-257.661	-257.733	-257.847		-257.907	-257.939	-257.907	-257.847	-257.869	-257.847	-257.783	-257.767	-257.752	-257.721	-257.690	-257.597	-257.562	-257.406		
EXG GROUND LEVEL AT TOE LOCATION OF DFC TRACK	-257.146	-257.146	-257.314	-257.286	-257.370	-257.213	-257.281	-257.518	-257.290	-257.375	-257.375	-256.090	-257.509	-257.178	-257.034	-257.131	-257.131	-256.953	-257.160	-257.125	-257.125	-256.703	-257.125	-257.121	-257.121	-257.006	-257.006	-257.006	-257.006	-257.006	-257.006	
DIFFERENCE BETWEEN DFC FORMATION LEVEL AND EXG.FORMATION LEVEL (PFL-EFL)	0.451	0.451	0.436	0.421	0.406	0.391	0.368	0.353	0.348	0.320	0.320	0.225	0.253	0.230	0.202	0.190	0.178	0.173	0.173	0.147	0.111	0.100	0.096	0.091	0.088	0.088	0.088	0.088	0.088	0.088	0.088	
DFC FORMATION LEVEL (PFL)	-258.664	-258.664	-258.433	-258.402	-258.371	-258.340	-258.309	-258.278	-258.247	-258.216	-258.216	-258.093	-258.062	-258.031	-258.000	-257.969	-257.938	-257.907	-257.876	-257.845	-257.814	-257.783	-257.752	-257.721	-257.690	-257.659	-257.628	-257.597	-257.566	-257.535	-257.504	
EXG. FORMATION LEVEL OF EXG IR UP MAIN LINE (EFL)	-258.013	-258.013	-257.997	-257.981	-257.965	-257.949	-257.941	-257.925	-257.889	-257.886	-257.886	-257.868	-257.809	-257.801	-257.798	-257.779	-257.760	-257.734	-257.729	-257.729	-257.734	-257.714	-257.687	-257.661	-257.633	-257.606	-257.579	-257.552	-257.525	-257.498	-257.471	
DIFFERENCE BETWEEN DFC RAIL LEVEL AND EXG. RAIL LEVEL (PRL - ERL)	0.494	0.494	0.478	0.463	0.449	0.433	0.410	0.396	0.390	0.362	0.362	0.267	0.295	0.271	0.244	0.231	0.219	0.215	0.189	0.153	0.142	0.138	0.133	0.130	0.130	0.130	0.130	0.130	0.130	0.130	0.130	
DFC RAIL LEVEL (PRL)	-259.178	-259.178	-259.147	-259.116	-259.085	-259.054	-259.023	-258.992	-258.961	-258.931	-258.931	-258.807	-258.776	-258.745	-258.714	-258.683	-258.652	-258.621	-258.590	-258.559	-258.528	-258.497	-258.466	-258.435	-258.404	-258.373	-258.342	-258.311	-258.280	-258.249	-258.218	
EXG.RAIL LEVEL OF NEAREST IR UP MAIN LINE(ERL)	-258.685	-258.685	-258.669	-258.653	-258.637	-258.621	-258.613	-258.597	-258.571	-258.576	-258.576	-258.540	-258.481	-258.473	-258.470	-258.451	-258.432	-258.406	-258.401	-258.406	-258.386	-258.360	-258.333	-258.305	-258.278	-258.251	-258.224	-258.197	-258.170	-258.143	-258.116	
EQUIVALENT CHAINAGE ON DFC TRACK	1246377.7	1246377.7	1246397.7	1246417.7	1246437.7	1246457.7	1246477.7	1246497.7	1246517.7	1246537.7	1246557.7	1246577.7	1246597.7	1246617.7	1246637.7	1246657.7	1246677.7	1246697.7	1246717.7	1246737.7	1246757.7	1246777.7	1246797.7	1246817.7	1246837.7	1246857.7	1246877.7	1246897.7	1246917.7	1246937.7	1246957.7	
EXISTING IR CHAINAGE	355500.0	355500.0	355520.0	355540.0	355560.0	355580.0	355600.0	355620.0	355640.0	355660.0	355680.0	355700.0	355720.0	355740.0	355760.0	355780.0	355800.0	355820.0	355840.0	355860.0	355880.0	355900.0	355920.0	355940.0	355960.0	355980.0	356000.0					

L - SECTION